




CORTE A-A TRAMO 1 (N1→N2 desde el cimiento y N2→N3 típico)

ESC. 1:25

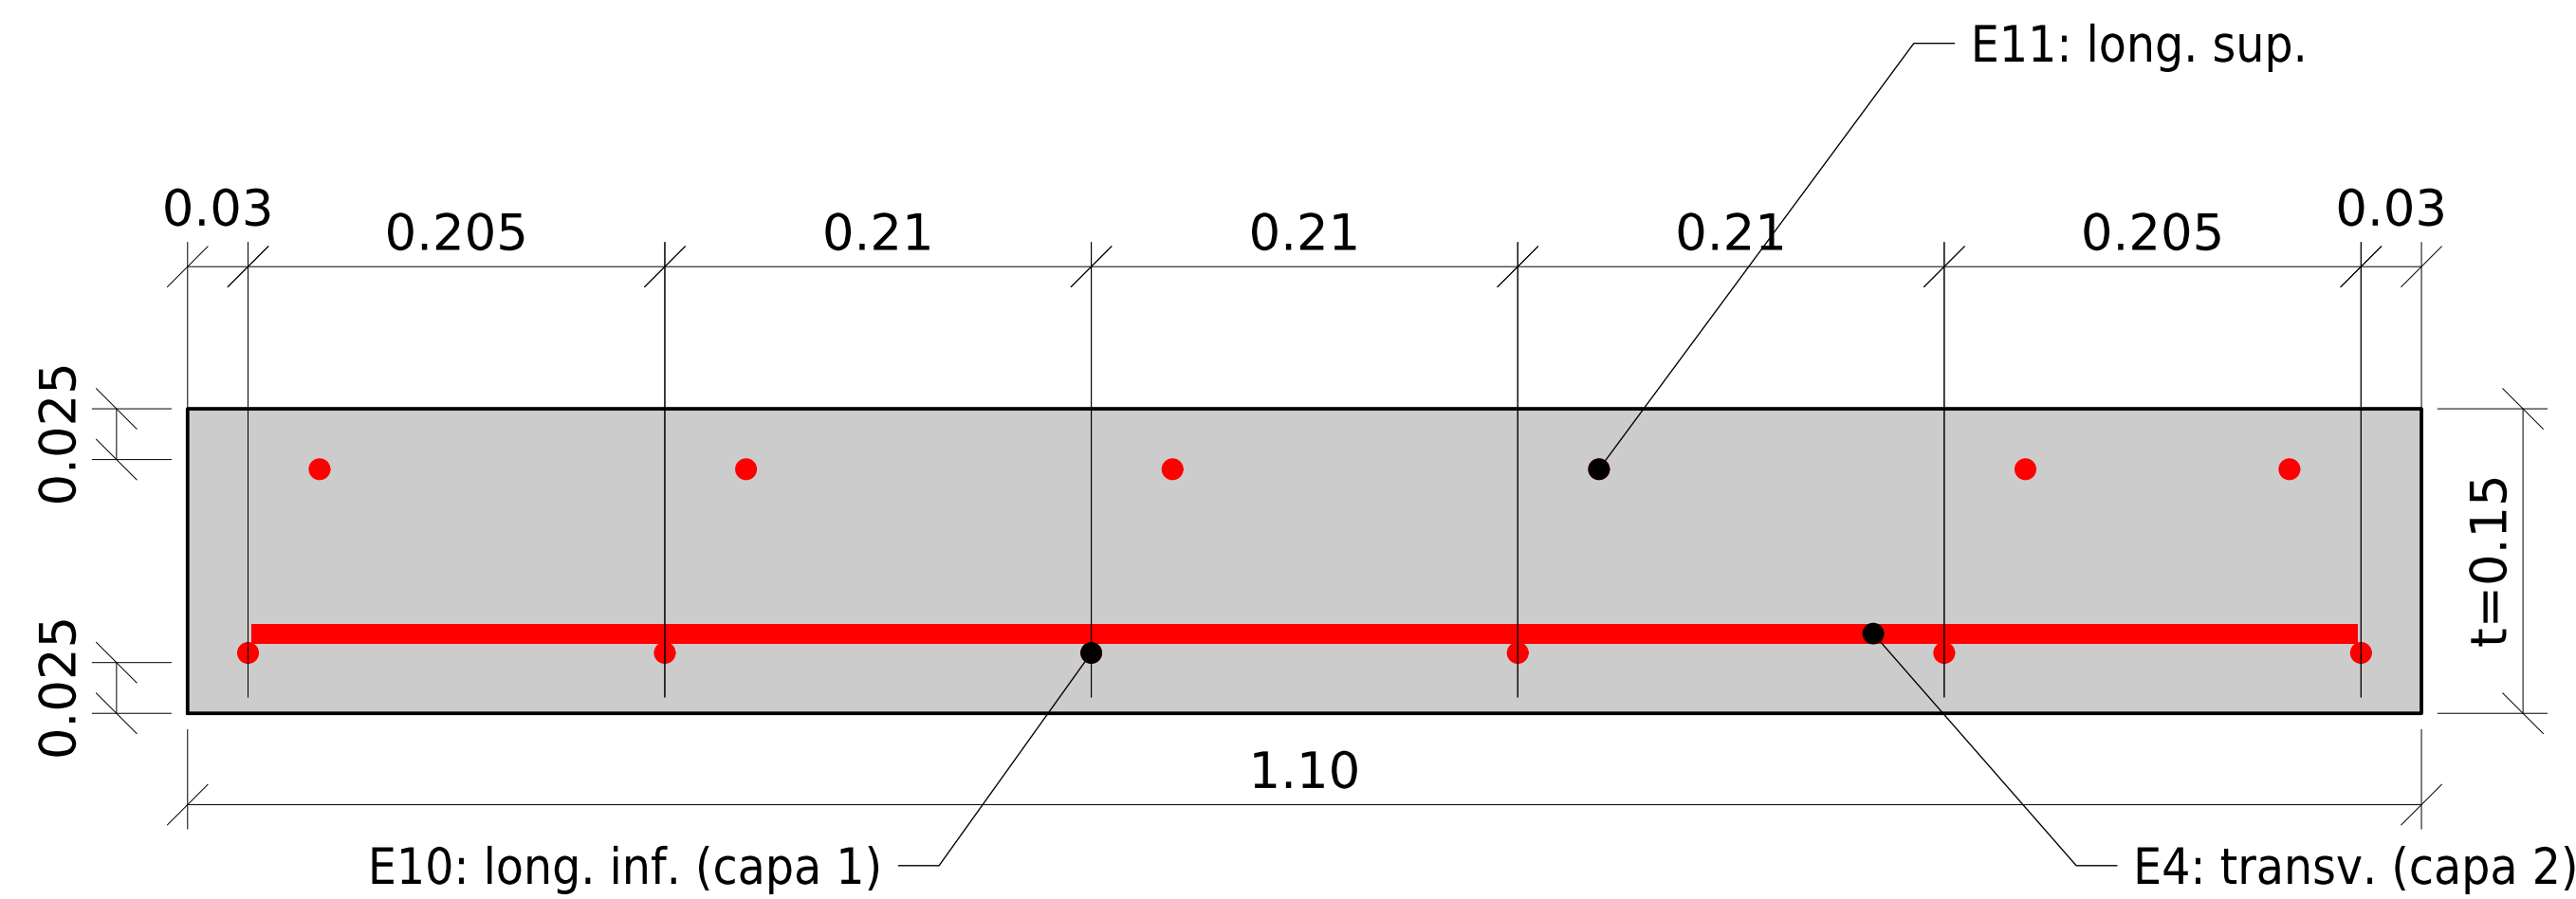

(capa 2 apoyada sobre la capa 1; recubrimiento libre 2.5 cm)

SECCIÓN TÍPICA DE TRAMO (perpendicular a la losa)

ESC. 1:10 (tramo 1, N2→N3)

CUADRO DE TRAMOS (medido del modelo, m)

PISO	TRAMO 1: contrapasos / pasos	TRAMO 2: contrapasos / pasos	TOTAL	DESCANSO	LLEGADA
N1-N2	12 x 0.1684 / 11 x 0.255	7 x 0.1684 / 6 x 0.267	19 cp	NPT +2.02 L=1.25	NPT +3.20
N2-N3	8 x 0.1625 / 7 x 0.250	8 x 0.1625 / 7 x 0.250	16 cp	NPT +4.50 L=1.10	NPT +5.80
N3-N4	8 x 0.1625 / 7 x 0.250	8 x 0.1625 / 7 x 0.250	16 cp	NPT +7.10 L=1.10	NPT +8.40

CUADRO DE ACERO DE ES

CÓD.	
E1	Mecha cimiento, traslapa con s
E2	Long. inferior tramo 1 (N1-N2)
E3	Long. superior tramo 1 (N1-N2)
E4	Transversal tramo 1 y tramo 2
E5	Long. inferior tramo 2 (N1-N2)
E6	Long. superior tramo 2 (N1-N2)
E7	Long. inferior descanso (N1-N2)
E8	Transversal descanso y platafo
E9	Long. inferior plataforma (todos
E10	Long. inferior tramo 1 y tramo
E11	Long. superior tramo 1 y tramo
E12	Long. inferior descanso (N2-N3)
	TOTAL ACERO DE ESCALERA (0

TRAMOS: longitudes de los segmentos de la
Códigos E# en los cortes. Cantidades: todas

OBSERVACIONES DEL MODELO (n

- En el modelo el acero de escalera t
de 2.5 cm: en esta lámina se dibuja
- Las 6 mechas del modelo (la extre
reemplazan por 5 mechas centrada
- Nudo de llegada del tramo 2 (J1) te
vacío en el modelo que atraviesan
- Capa 2 (transversal) a 4.5 mm de e
en obra la transversal apoya sobre
- Acero superior sin barras transvers
- De