



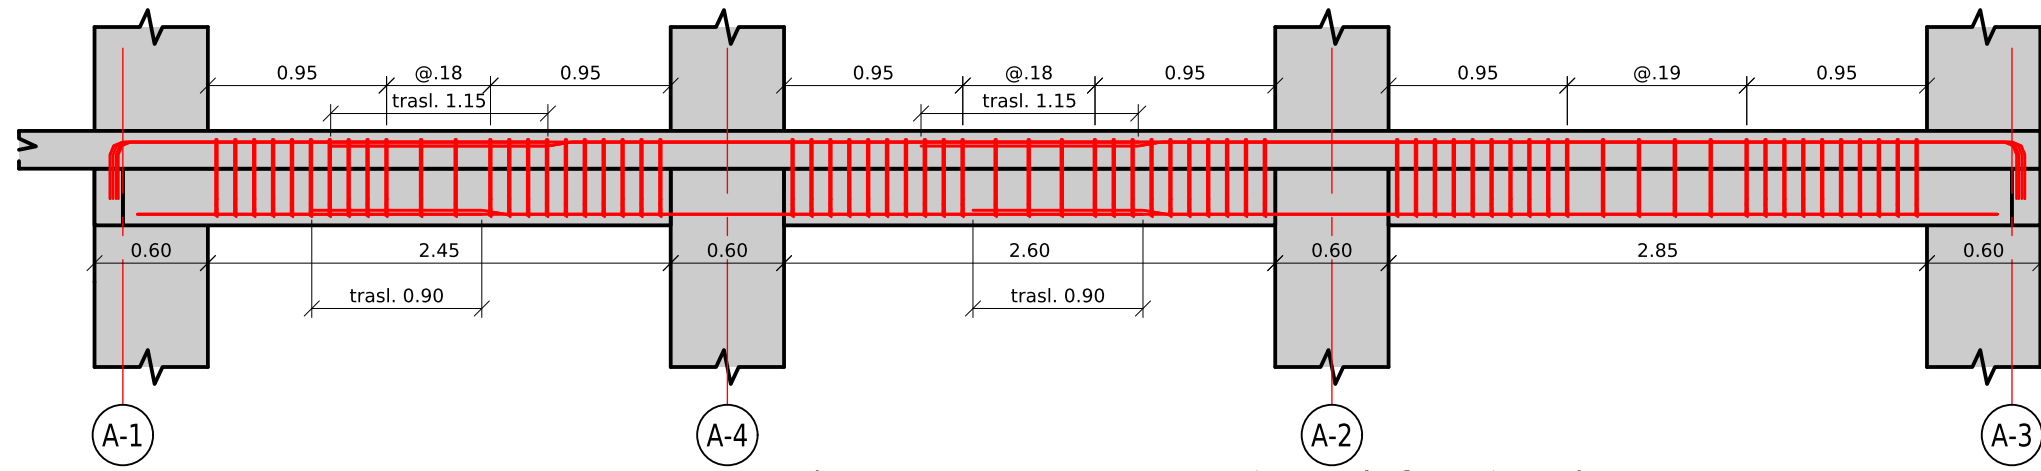


VIGA EJE N-1 (N2 a N5: sup. 5/3/3/3 Ø3/4", inf. 4 Ø3/4")

ESC. 1:40 - típica en todos los niveles; ver cuadro

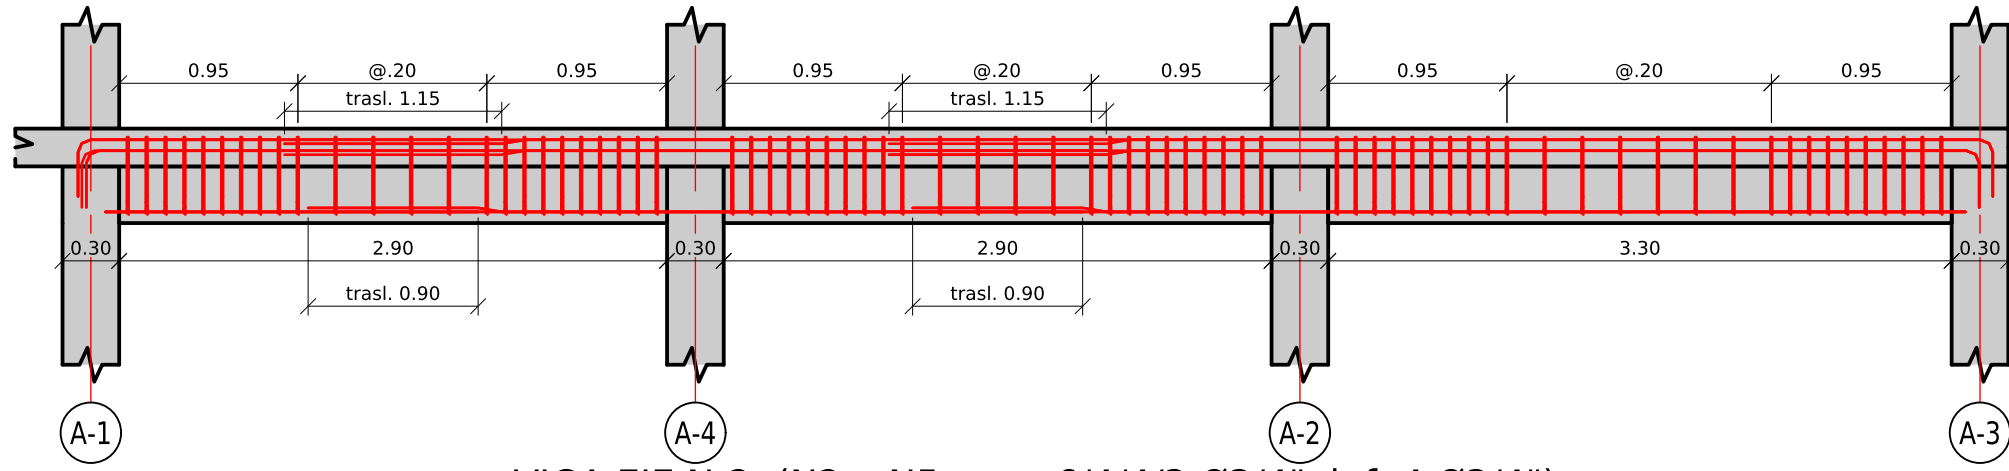

VIGA EJE N-2 (N2 a N5: sup. 6/4/4/3 Ø3/4", inf. 4 Ø3/4")

ESC. 1:40 - típica en todos los niveles; ver cuadro

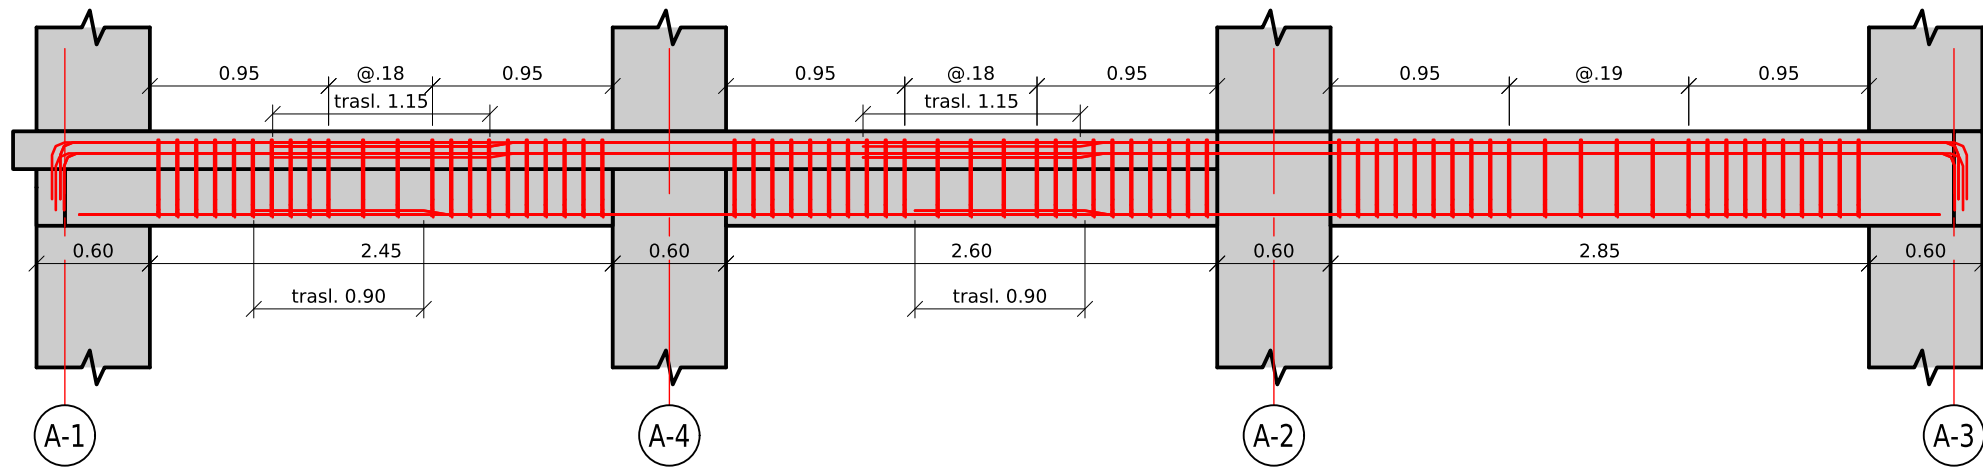

VIGA EJE N-3 (N2 a N5: sup. 6/4/3/3 Ø3/4", inf. 4 Ø3/4")


ESC. 1:40 - típica en todos los niveles; ver cuadro

CUADRO DE VIGAS POR NIVEL

EJE	NIVEL 2	NIVEL 3	NIVEL 4	NIVEL 5
N-1	VE-5	VE-3	VE-3	VE-3
N-2	VE-6	VE-4	VE-4	VE-3
N-3	VE-6	VE-4	VE-3	VE-3
A-1	VE-5	VE-3	VE-3	VE-3
A-4	VE-5	VE-3	VE-3	VE-3
A-2	VE-5	VE-3	VE-3	VE-3
A-3	VE-5	VE-3	VE-3	VE-3
COLLARÍN (N-4)	VCO	VCO	VCO	VCO


NOTAS - VIGAS

1. CONCRETO $f_c = \text{---}$ kg/cm² (COMPLETAR). ACERO ASTM A615 Gr. 60, $f_y = 4200$ kg/cm².
2. RECUBRIMIENTO libre al estribo 4 cm. Estribos cerrados con gancho 135°.
3. Barras corridas por eje; gancho estándar 90° en columnas extremas y en el extremo del volado.
4. Trasiapes fuera de nudos: sup. 1.15 m al centro del vano, inf. 0.90 m a 2h de la cara, alternados.
5. En el modelo Revit (nodo 12) varias capas quedaron desplazadas hasta 25 cm hacia el interior para evitar choques. Aquí se dibujan en su posición de diseño; corregir el modelo antes del metrado fino.
6. En los nudos, las barras de los ejes A pasan por dentro de las de los ejes N.

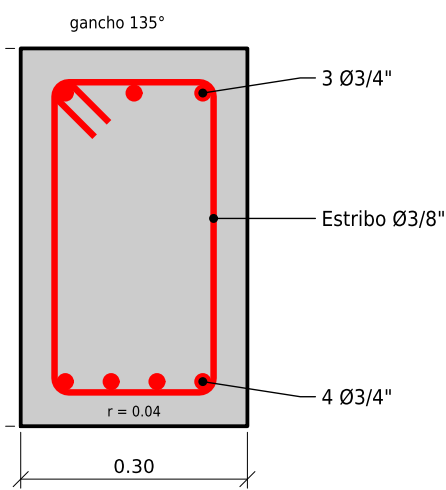


VE-3 0.30 x 0.50

ESC. 1:10

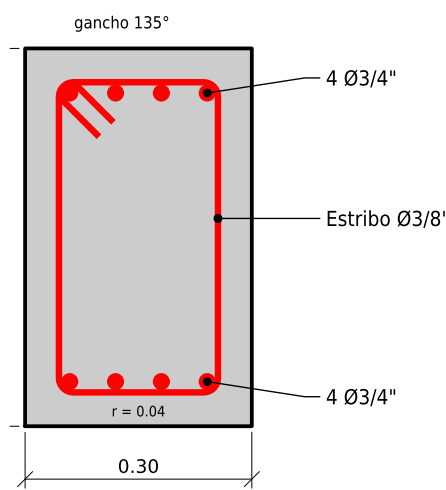


VE-4 0.30 x 0.50

ESC. 1:10

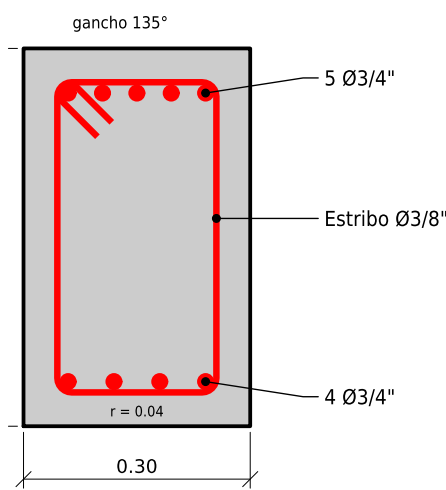


VE-5 0.30 x 0.50

ESC. 1:10

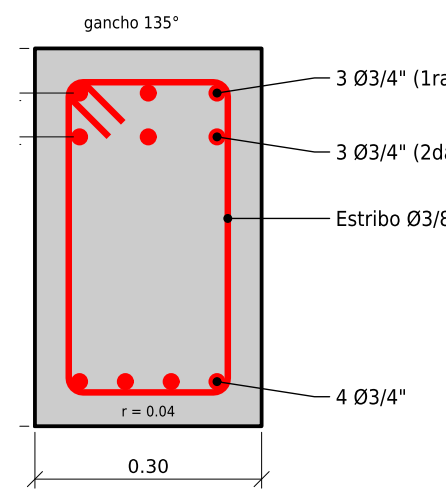

VE-6 0.30 x 0.50

ESC. 1:10

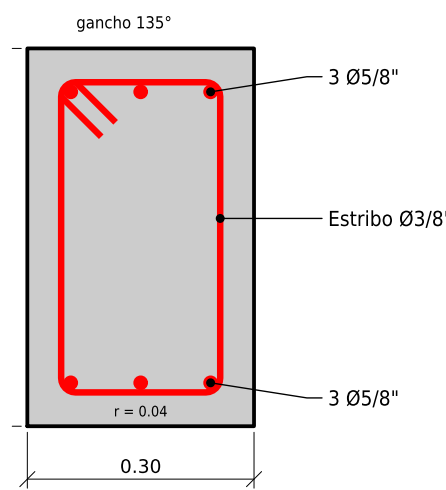


COLLARÍN VCO 0.30 x 0.50

ESC. 1:10


Estribos VE Ø3/8": 1@.05, 9@.10, rto. @.20 c/ext. (medido del modelo)

Estribos collarín Ø3/8": @.20 — Acero de vigas dibujado en su posición de diseño (E.060); ver nota 5.

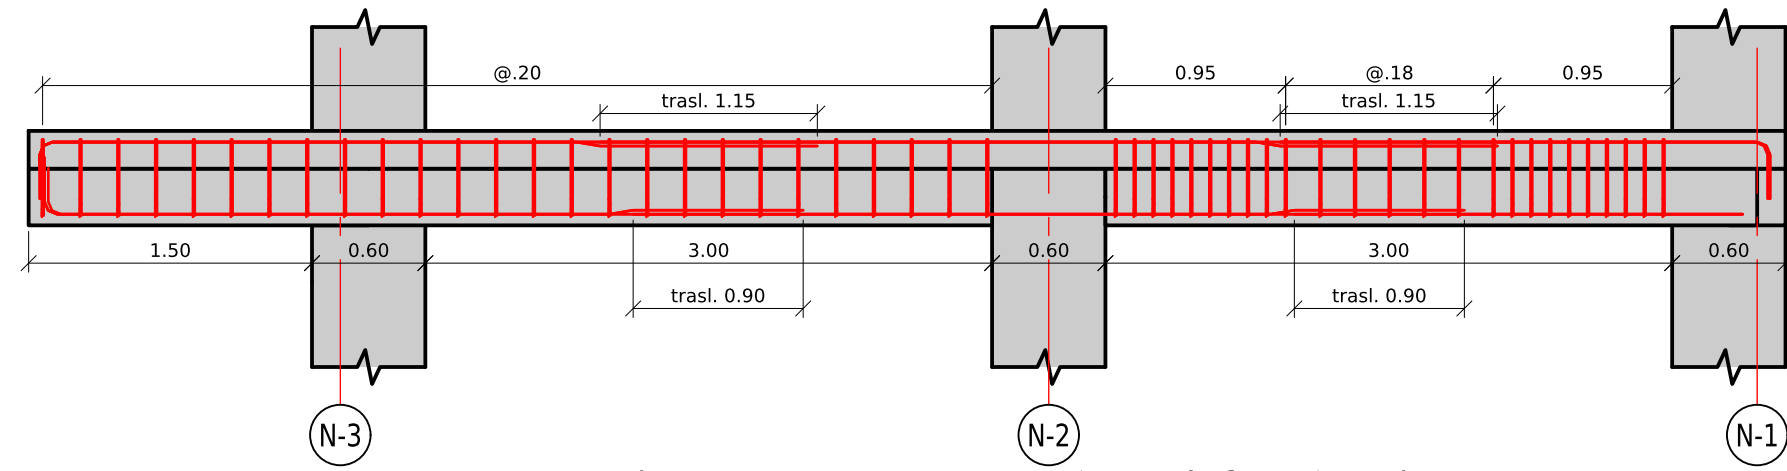


VIGA EJE A-1 (N2 a N5: sup. 5/3/3/3 Ø3/4", inf. 4 Ø3/4")

ESC. 1:40 - típica en todos los niveles; ver cuadro

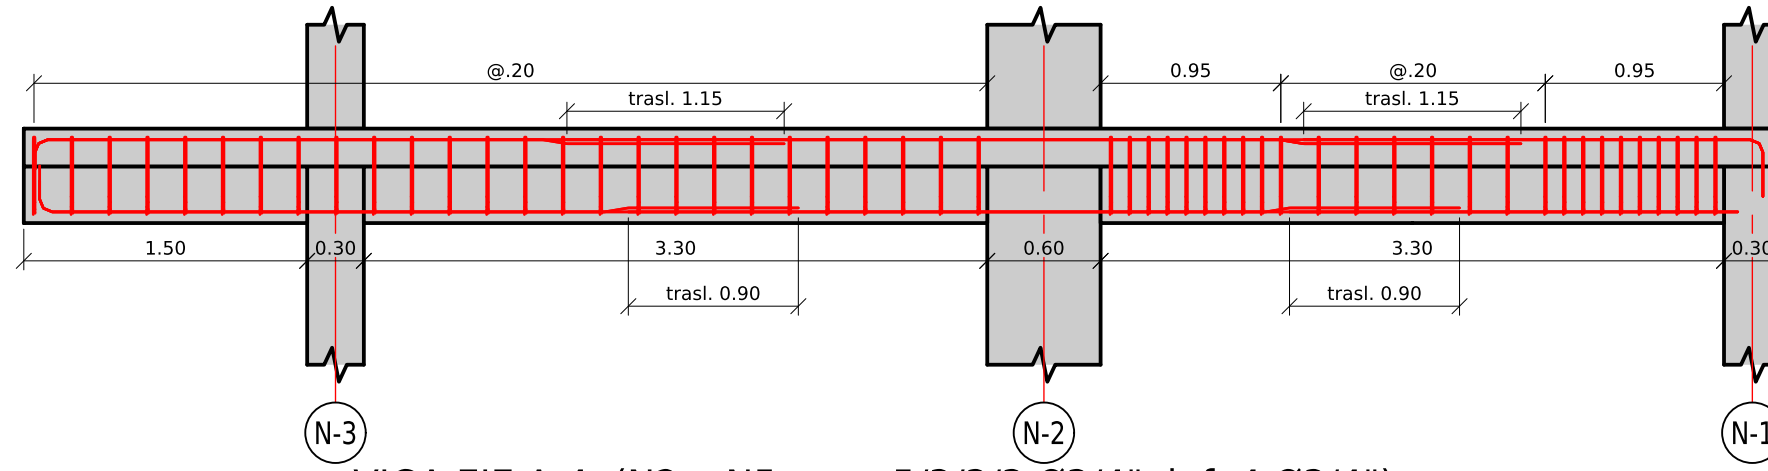


VIGA EJE A-4 (N2 a N5: sup. 5/3/3/3 Ø3/4", inf. 4 Ø3/4")

ESC. 1:40 - típica en todos los niveles; ver cuadro

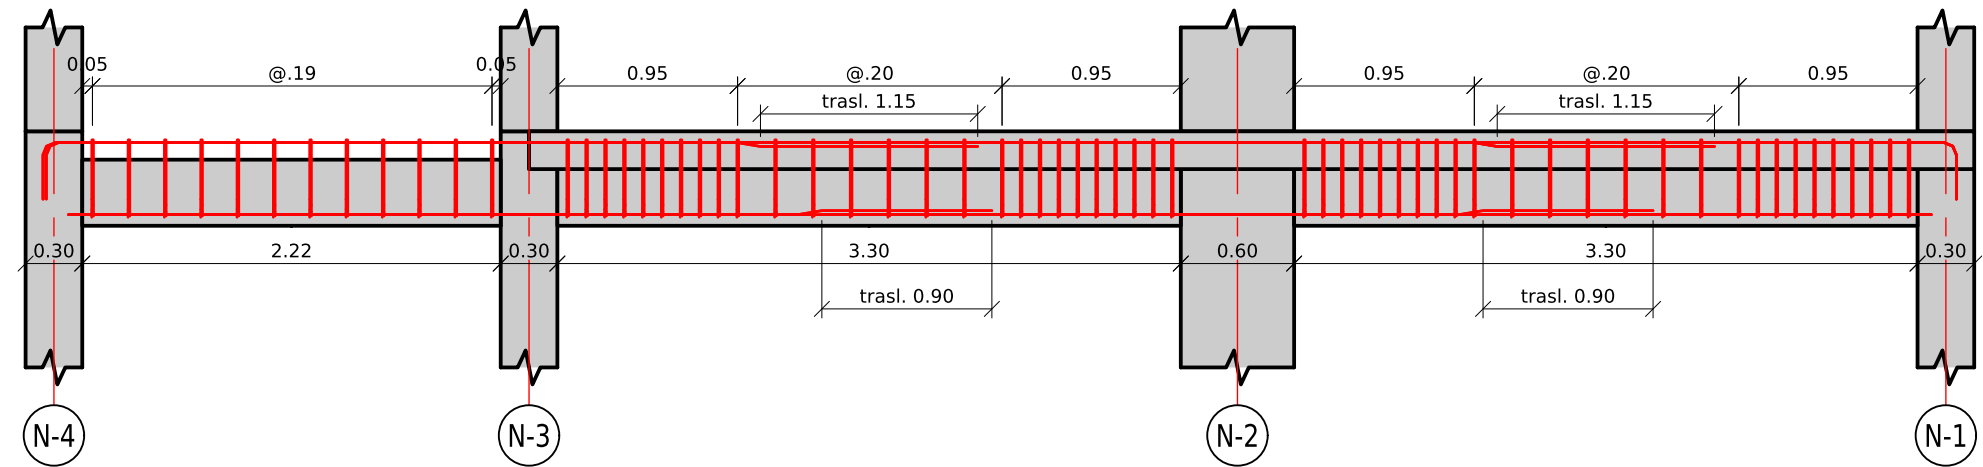

VIGA EJE A-2 (N2 a N5: sup. 5/3/3/3 Ø3/4", inf. 4 Ø3/4")

ESC. 1:40 - típica en todos los niveles; ver cuadro

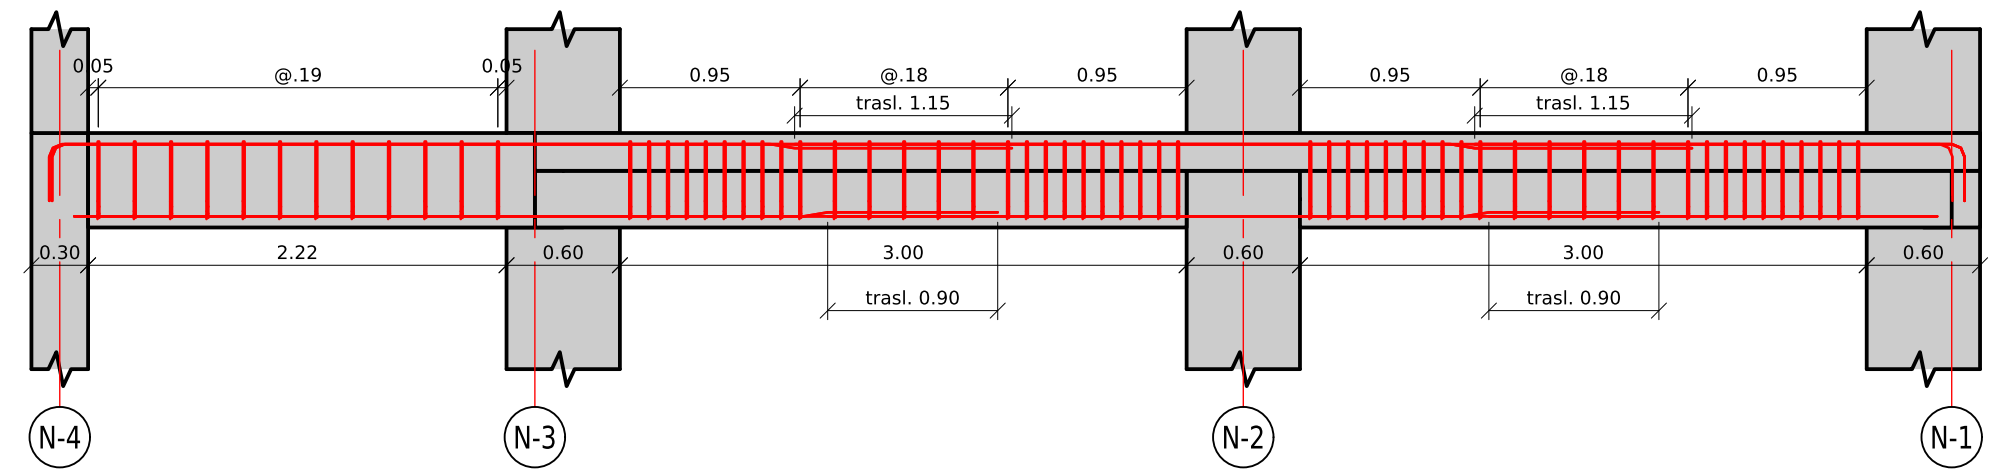

VIGA EJE A-3 (N2 a N5: sup. 5/3/3/3 Ø3/4", inf. 4 Ø3/4")

ESC. 1:40 - típica en todos los niveles; ver cuadro

PROYECTO:

CASA SAN JERÓNIMO - REDISEÑO ESTRUCTURAL 4 x 3

5 niveles (Cimentación -2.00, N1 ±0.00 ... N5 +11.00)

ESPECIALIDAD: ESTRUCTURAS

VIGAS DE ENTREPISO: ELEVACIONES,
SECCIONES TIPO Y CUADRO DE VIGAS

ESCALA: INDICADA

FECHA: SET. 2026

FUENTE: modelo IFC 'Proyect.sj.ifc'

(Revit 2027, IFC4, 26-09-2026)

PROFESIONAL RESPONSABLE:

CIP

REVISÓ:

LÁMINA

E-08