
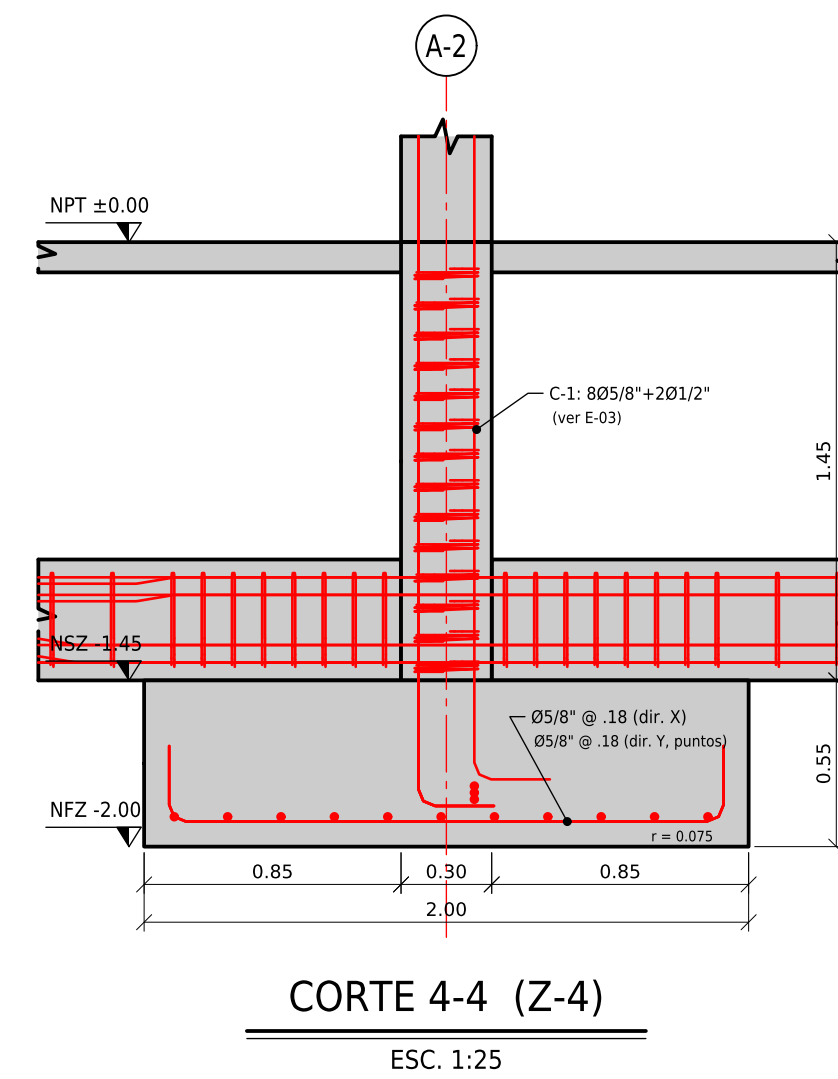
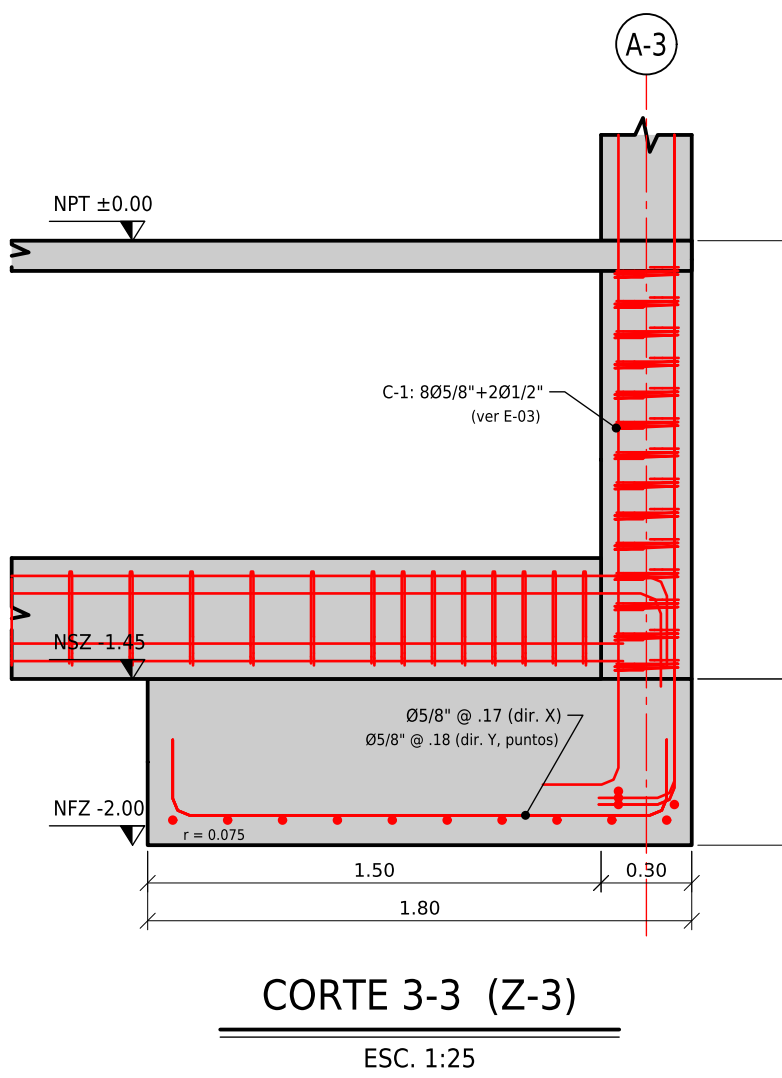
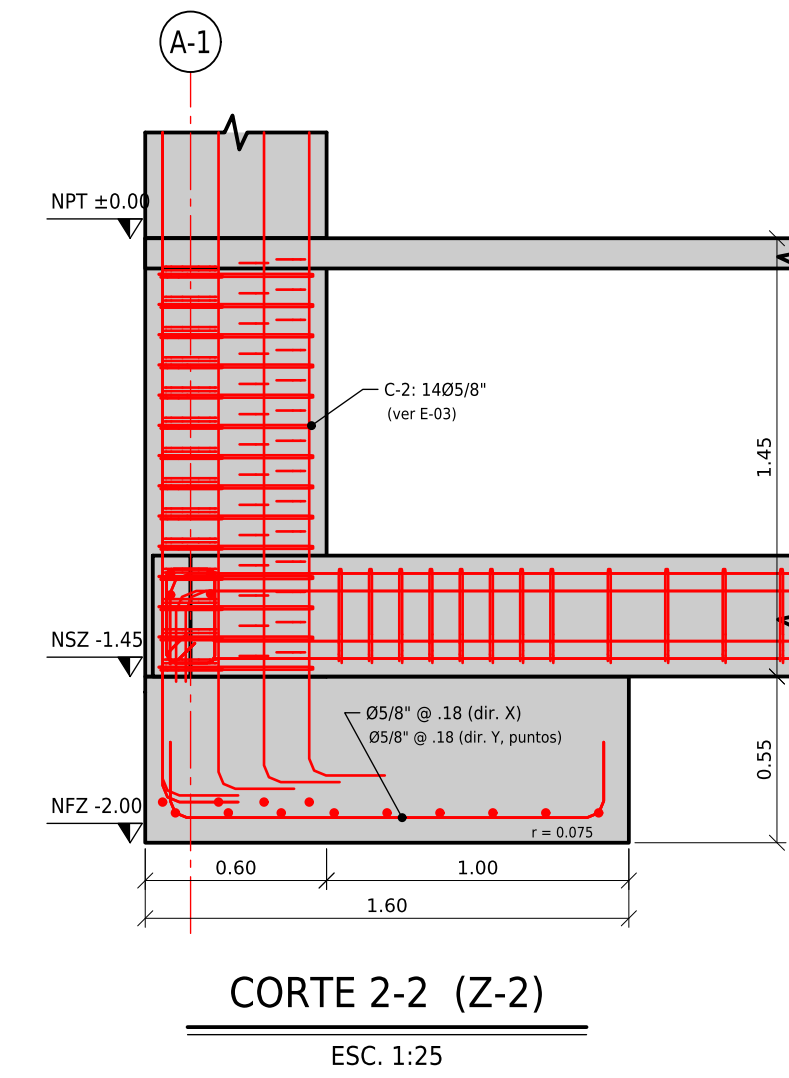
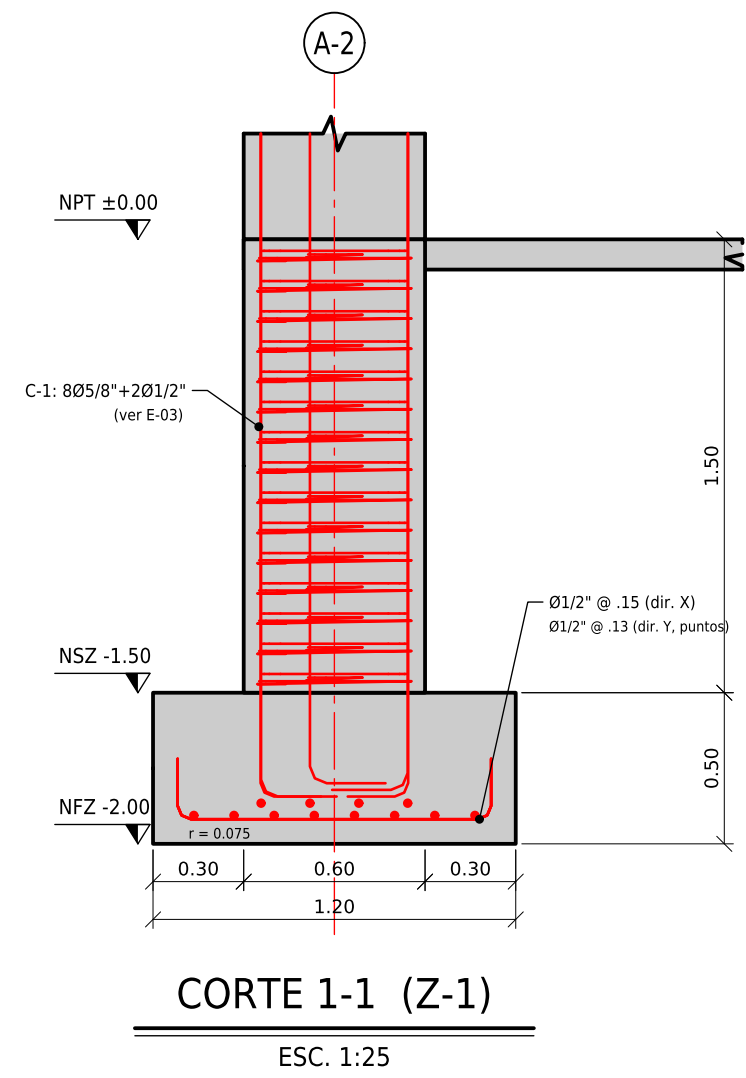
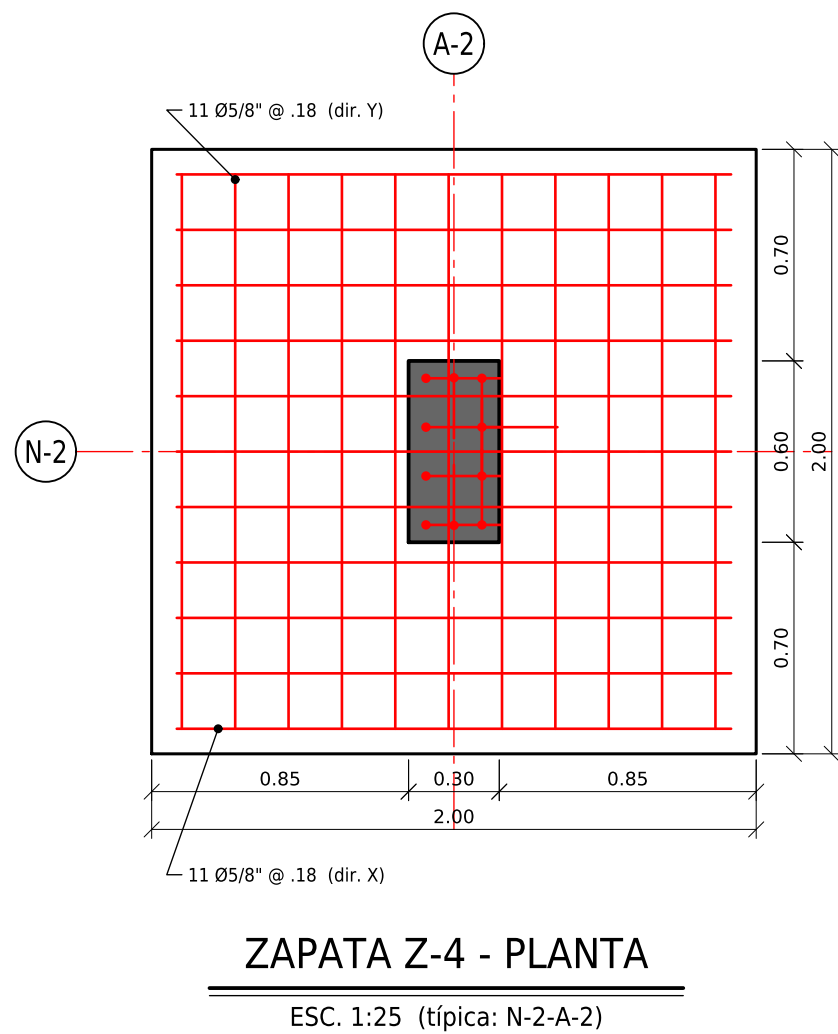
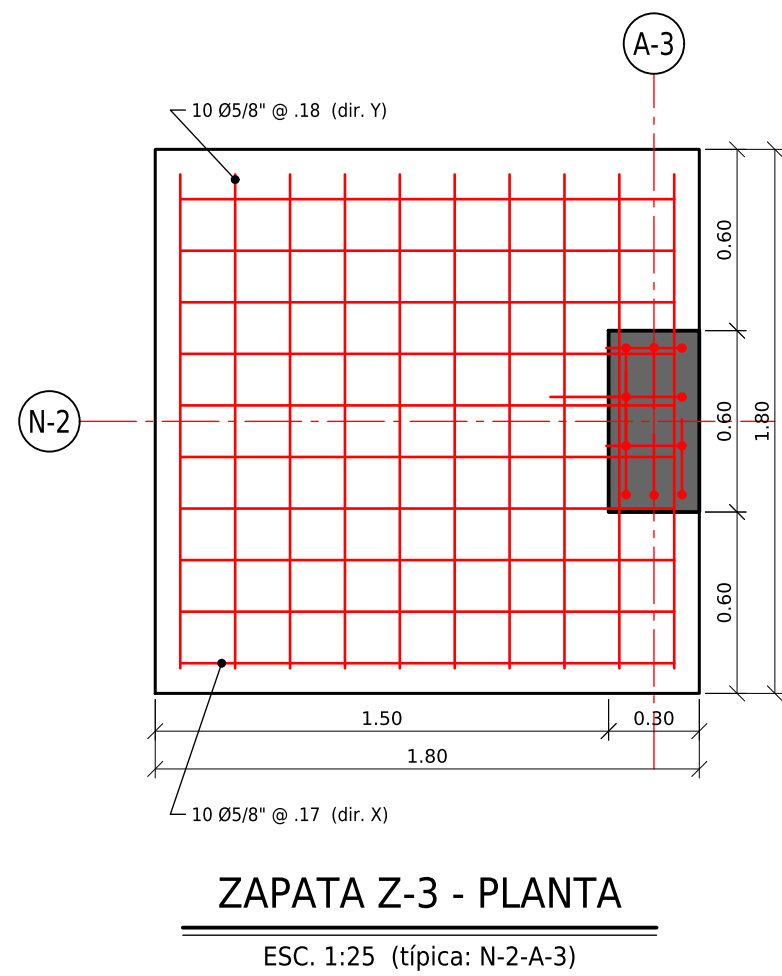
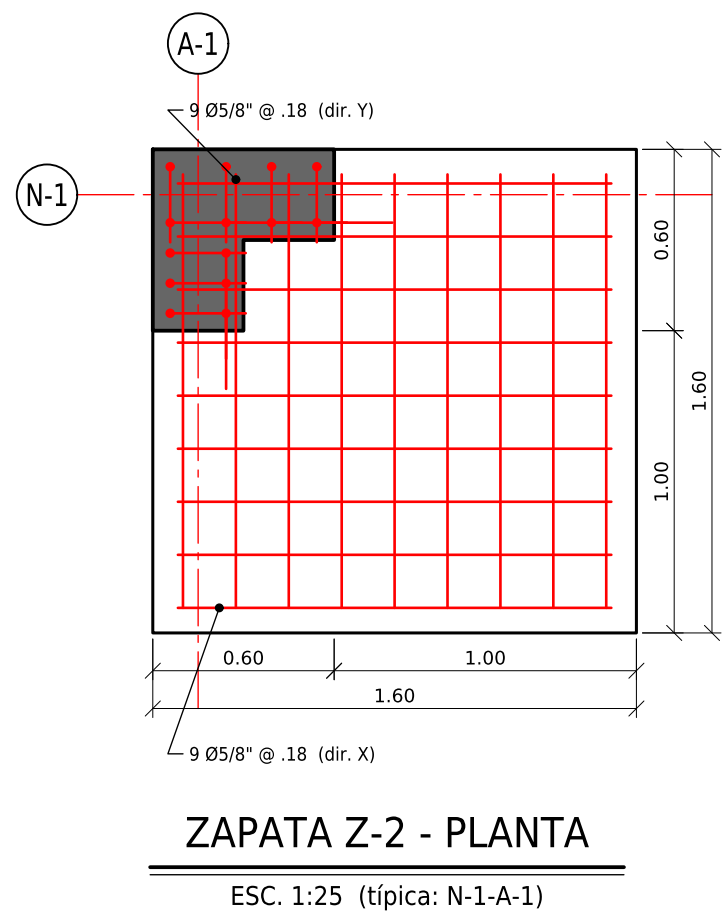
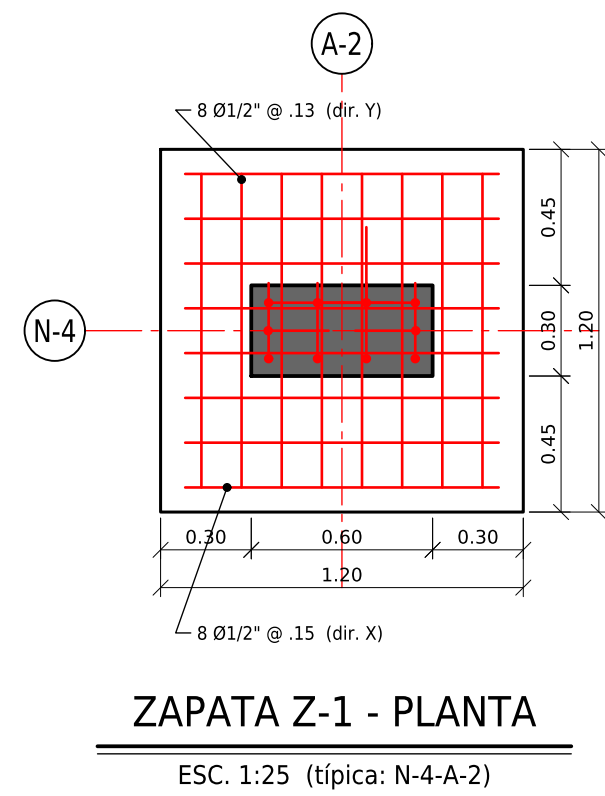





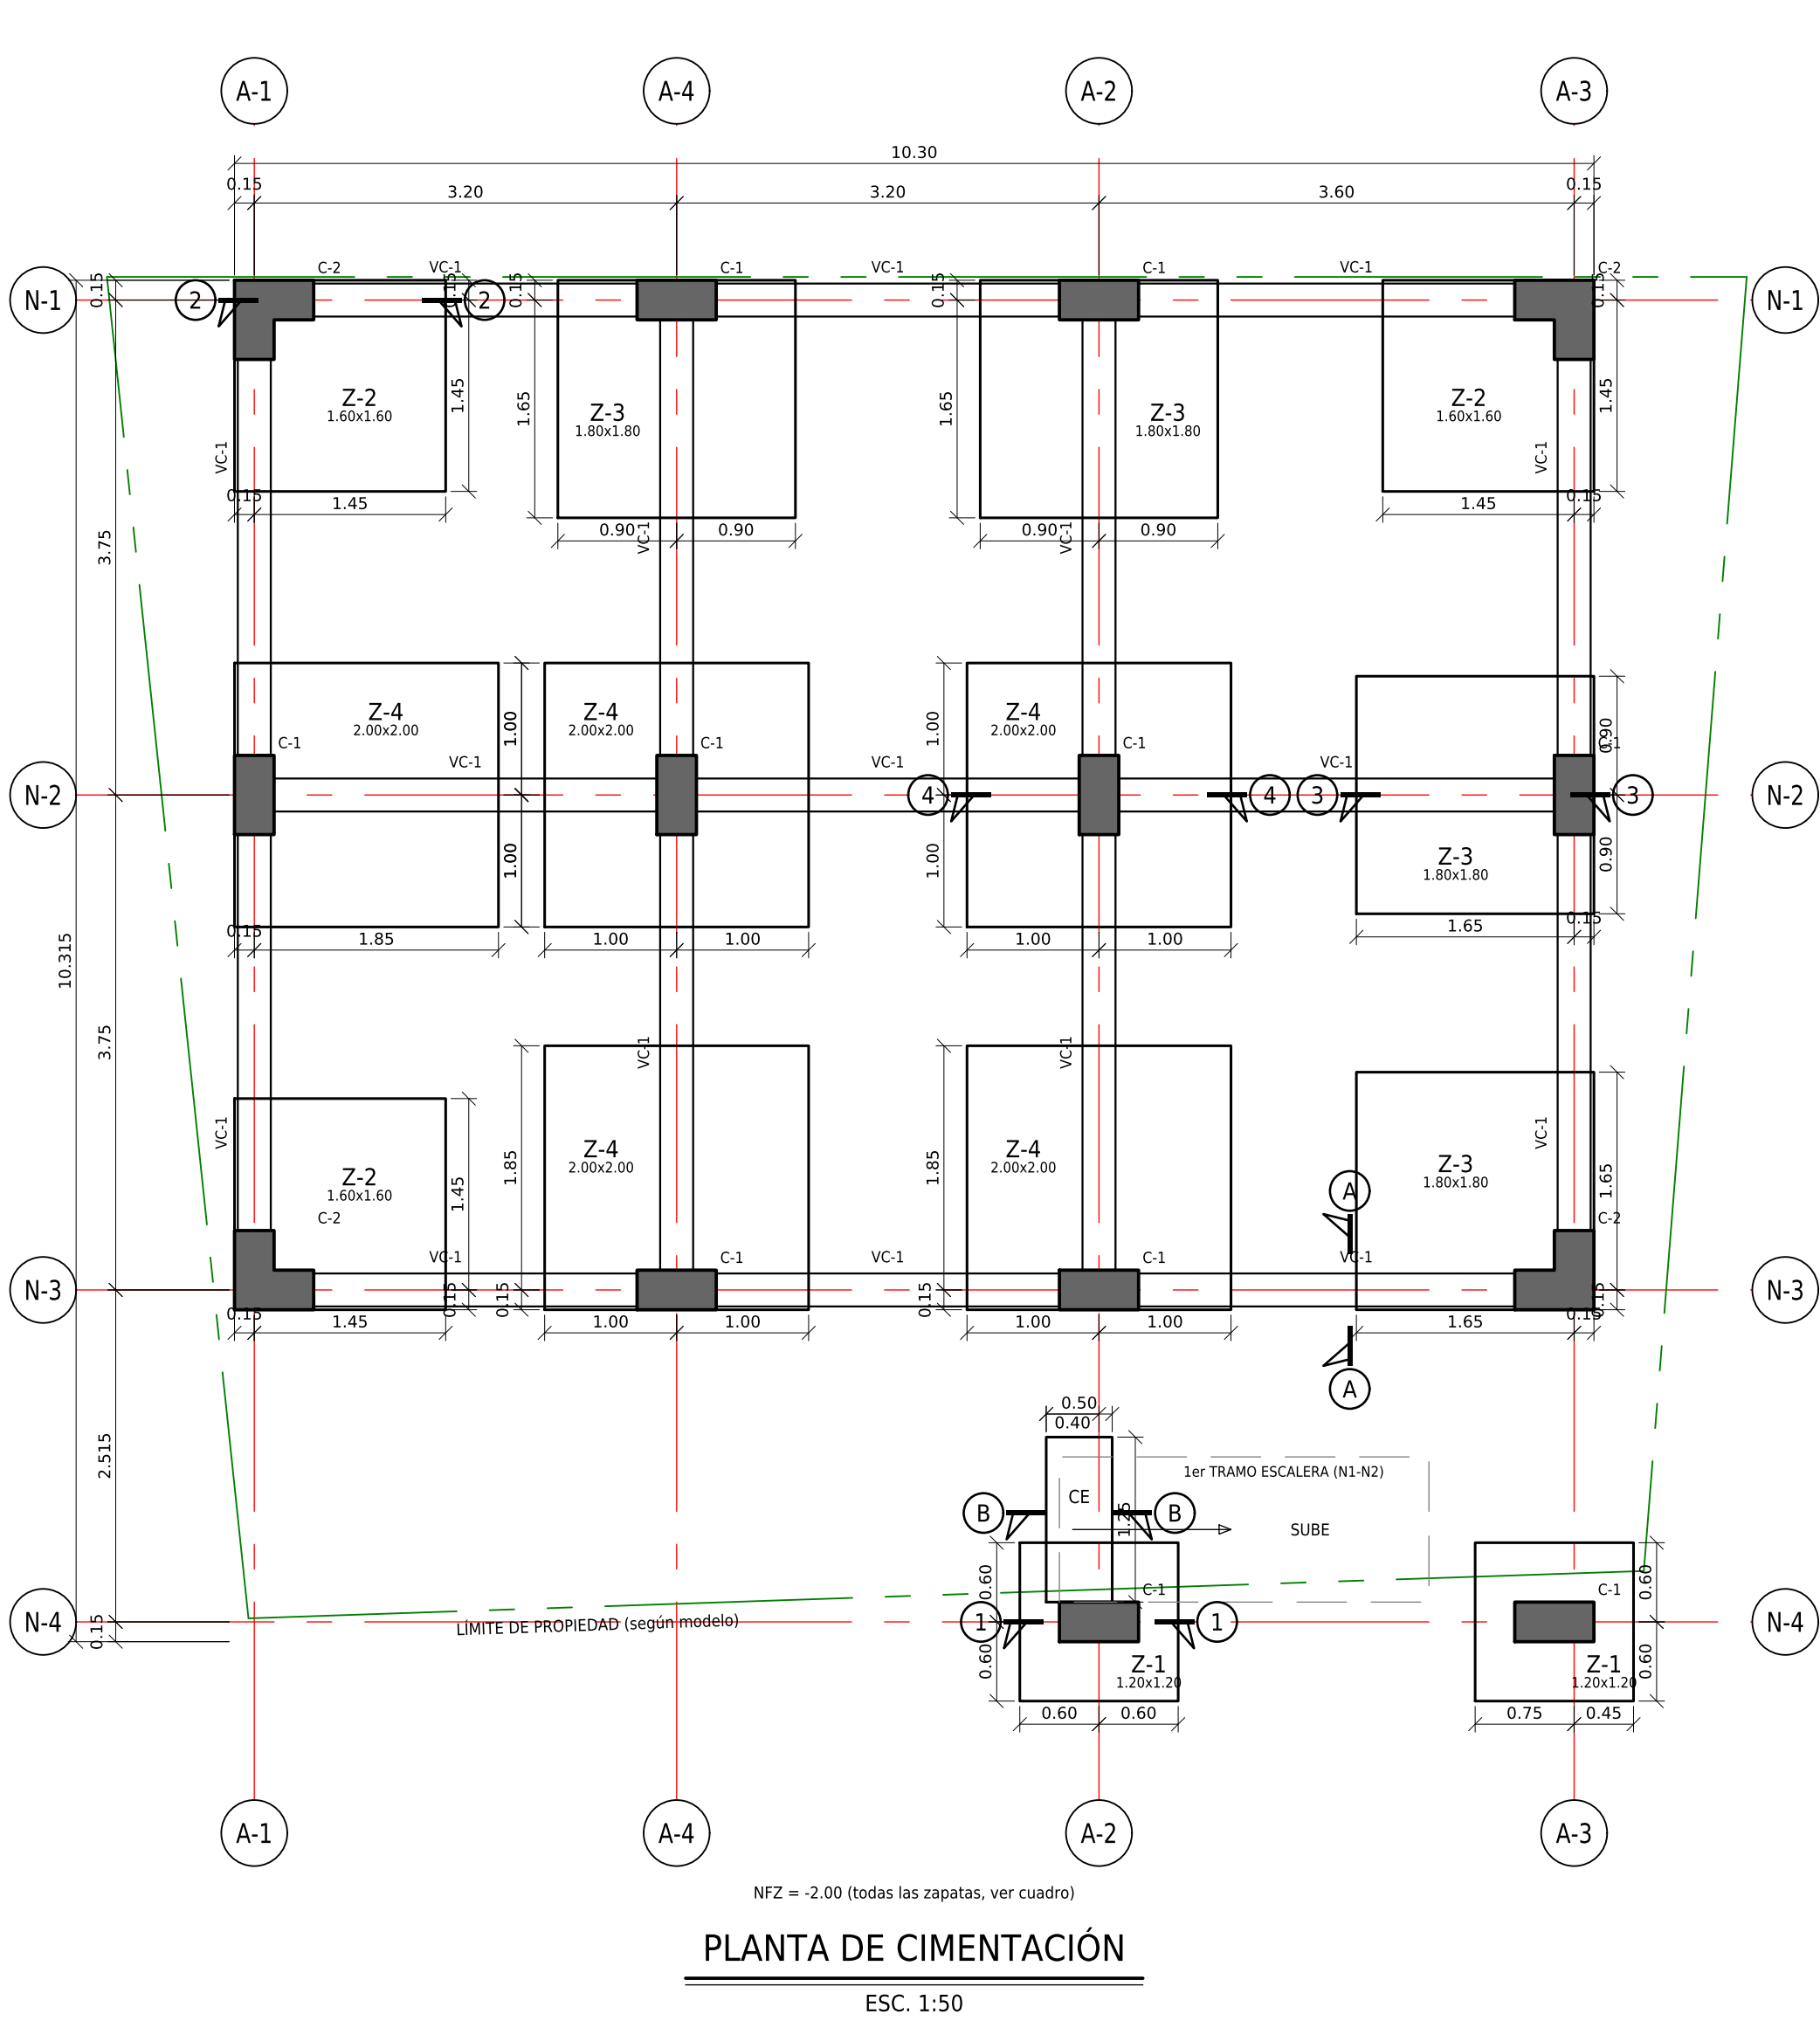


TIPO	CANT.	B x L (m)	h (m)	NFZ	PARRILLA DIR. X	PARRILLA DIR. Y	UBICACIÓN (ejes)
Z-1	2	1.20 x 1.20	0.50	-2.00	8 Ø1/2" @ .15	8 Ø1/2" @ .13	N-4/A-2, N-4/A-3
Z-2	3	1.60 x 1.60	0.55	-2.00	9 Ø5/8" @ .18	9 Ø5/8" @ .17-18	N-1/A-1, N-1/A-3, N-3/A-1
Z-3	4	1.80 x 1.80	0.55	-2.00	10 Ø5/8" @ .17-18	10 Ø5/8" @ .17-18	N-1/A-2, N-1/A-4, N-2/A-3, N-3/A-3
Z-4	5	2.00 x 2.00	0.55	-2.00	11 Ø5/8" @ .18	11 Ø5/8" @ .18	N-2/A-1, N-2/A-2, N-2/A-4, N-3/A-2, N-3/A-4
CE	1	0.50 x 1.25	1.00	-1.00	5 mechas Ø3/8"	—	arranque escalera

Dir. X: paralela a los ejes N (N-1 ... N-4). Dir. Y: paralela a los ejes A. Separación medida del modelo (m).

ELEMENTO	CONCRETO (m³)	ACERO (kg)	DETALLE ACERO
Zapatas (14)	23.79	852.0	Ø1/2": 44.5, Ø5/8": 807.5
Vigas de cimentación (17)	5.37	1535.0	Ø3/4": 1295.7, Ø3/8": 239.3
Cimiento de escalera	0.62	3.7	Ø3/8": 3.7
TOTAL	29.79	2390.6	arranques de columna: ver E-03

- ESPECIFICACIONES TÉCNICAS - CIMENTACIÓN
- CONCRETO $f_c = 210 \text{ kg/cm}^2$ en zapatas, vigas de cimentación y cimiento de escalera; solados $f_c = 100 \text{ kg/cm}^2$.
 - ACERO corrugado ASTM A615 Grado 60, $f_y = 4200 \text{ kg/cm}^2$.
 - RECUBRIMIENTOS: zapatas 7.5 cm (contra terreno); vigas de cimentación 4 cm; columnas ver E-03.
 - SUELO (EMS): $q_{adm} = 1.22 - 1.31 \text{ kg/cm}^2$ a $D_f = 2.00 \text{ m}$, $NFZ = -2.00 \text{ m}$. El cimiento de escalera se funda a -1.00 m : confirmar la capacidad portante a esa profundidad antes de vaciar.
 - Parrilla de zapatas en dos capas, gancho a 90° hacia arriba en ambos extremos. Arranques de columna con pata de 12 db apoyada sobre la parrilla, hacia el interior de la zapata.
 - Vigas de cimentación: barras corridas por eje, gancho estándar en columnas extremas. Traslapes fuera de nudos: superiores 1.15 m al centro del vano, inferiores 0.90 m a 2h de la cara de columna, alternados.
 - Cotas y niveles en metros. $NPT \pm 0.00 = \text{Nivel 1}$. Ejes según modelo (orden A-1, A-4, A-2, A-3).
 - Plano generado del modelo IFC 'Project sj.ifc' (Revit 2027). Dimensiones y acero tal como están modelados.

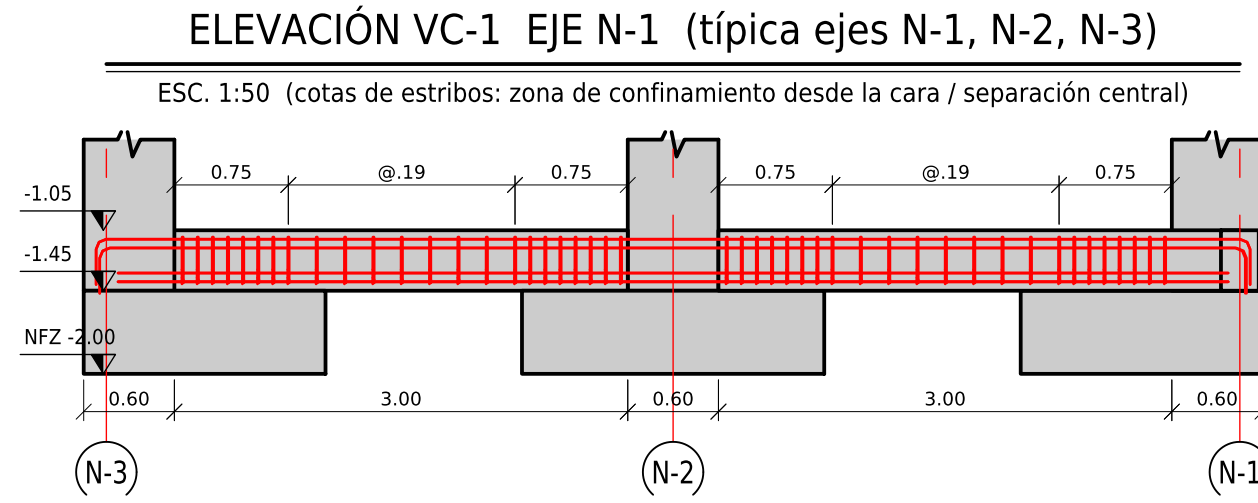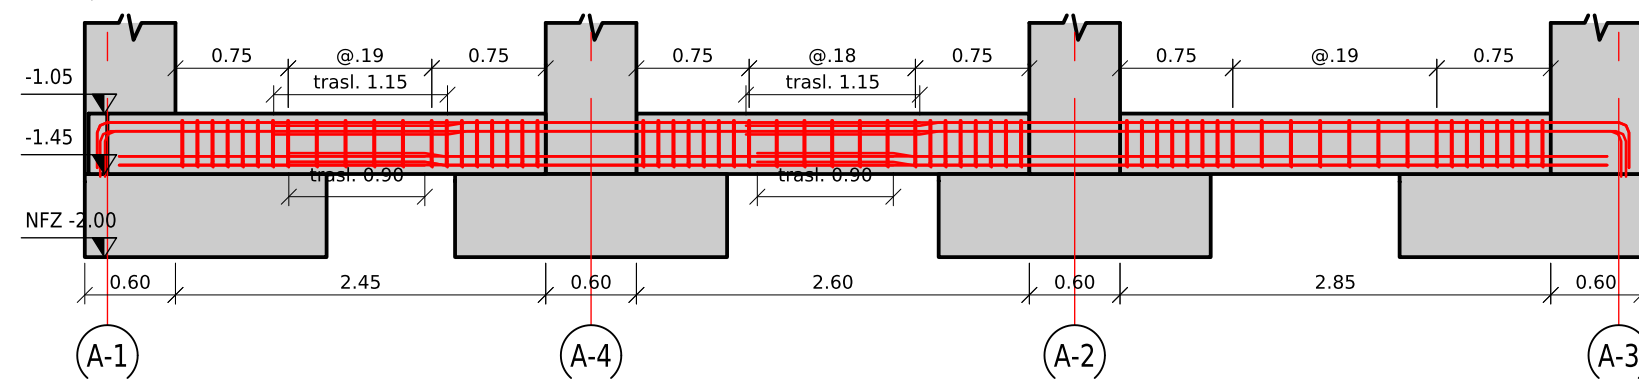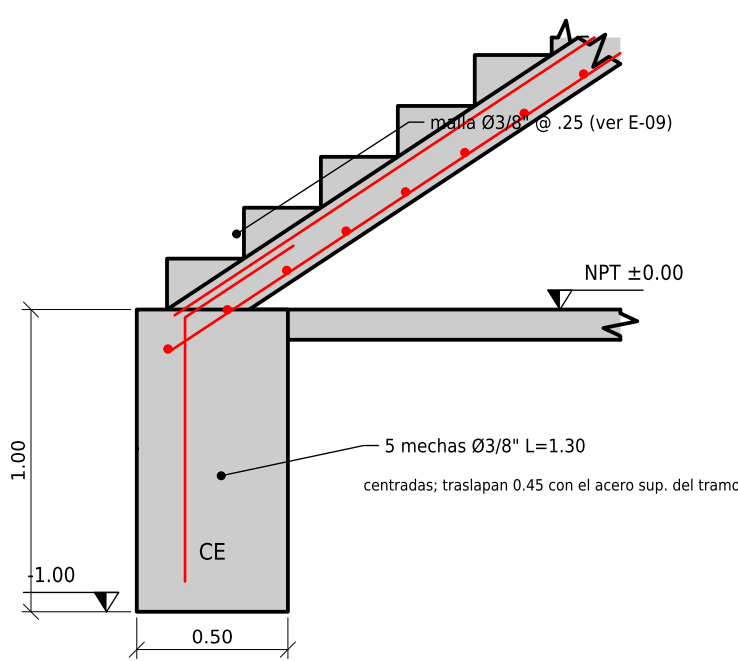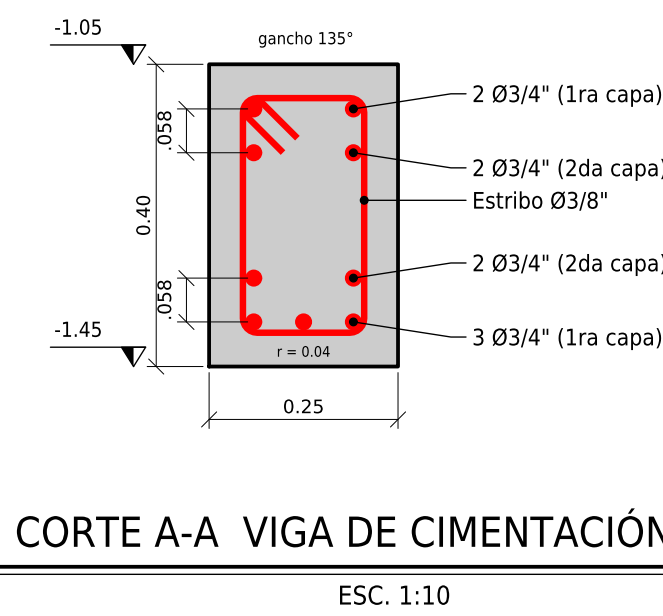

- LEYENDA
- Columna (C-1 rectangular 0.30x0.60 / C-2 en L 0.60x0.60x0.30)
 - Zapata aislada (Z-#) / cimiento de escalera (CE)
 - Viga de cimentación VC-1 0.25x0.40 (fondo -1.45, tope -1.05)
 - Límite de propiedad (según modelo)
 - Acero de refuerzo

PROYECTO: CASA SAN JERÓNIMO - REDISEÑO ESTRUCTURAL 4 x 3 5 niveles (Cimentación -2.00, N1 ±0.00 ... N5 +11.00)		
ESPECIALIDAD: ESTRUCTURAS CIMENTACIÓN: PLANTA, DETALLES DE ZAPATAS, VIGA DE CIMENTACIÓN Y CUADRO DE ZAPATAS		
ESCALA: INDICADA FECHA: SET. 2026	FUENTE: modelo IFC 'Project sj.ifc' (Revit 2027, IFC4, 26-09-2026)	LÁMINA E-01
PROFESIONAL RESPONSABLE: CIP _____	REVISÓ: _____	