



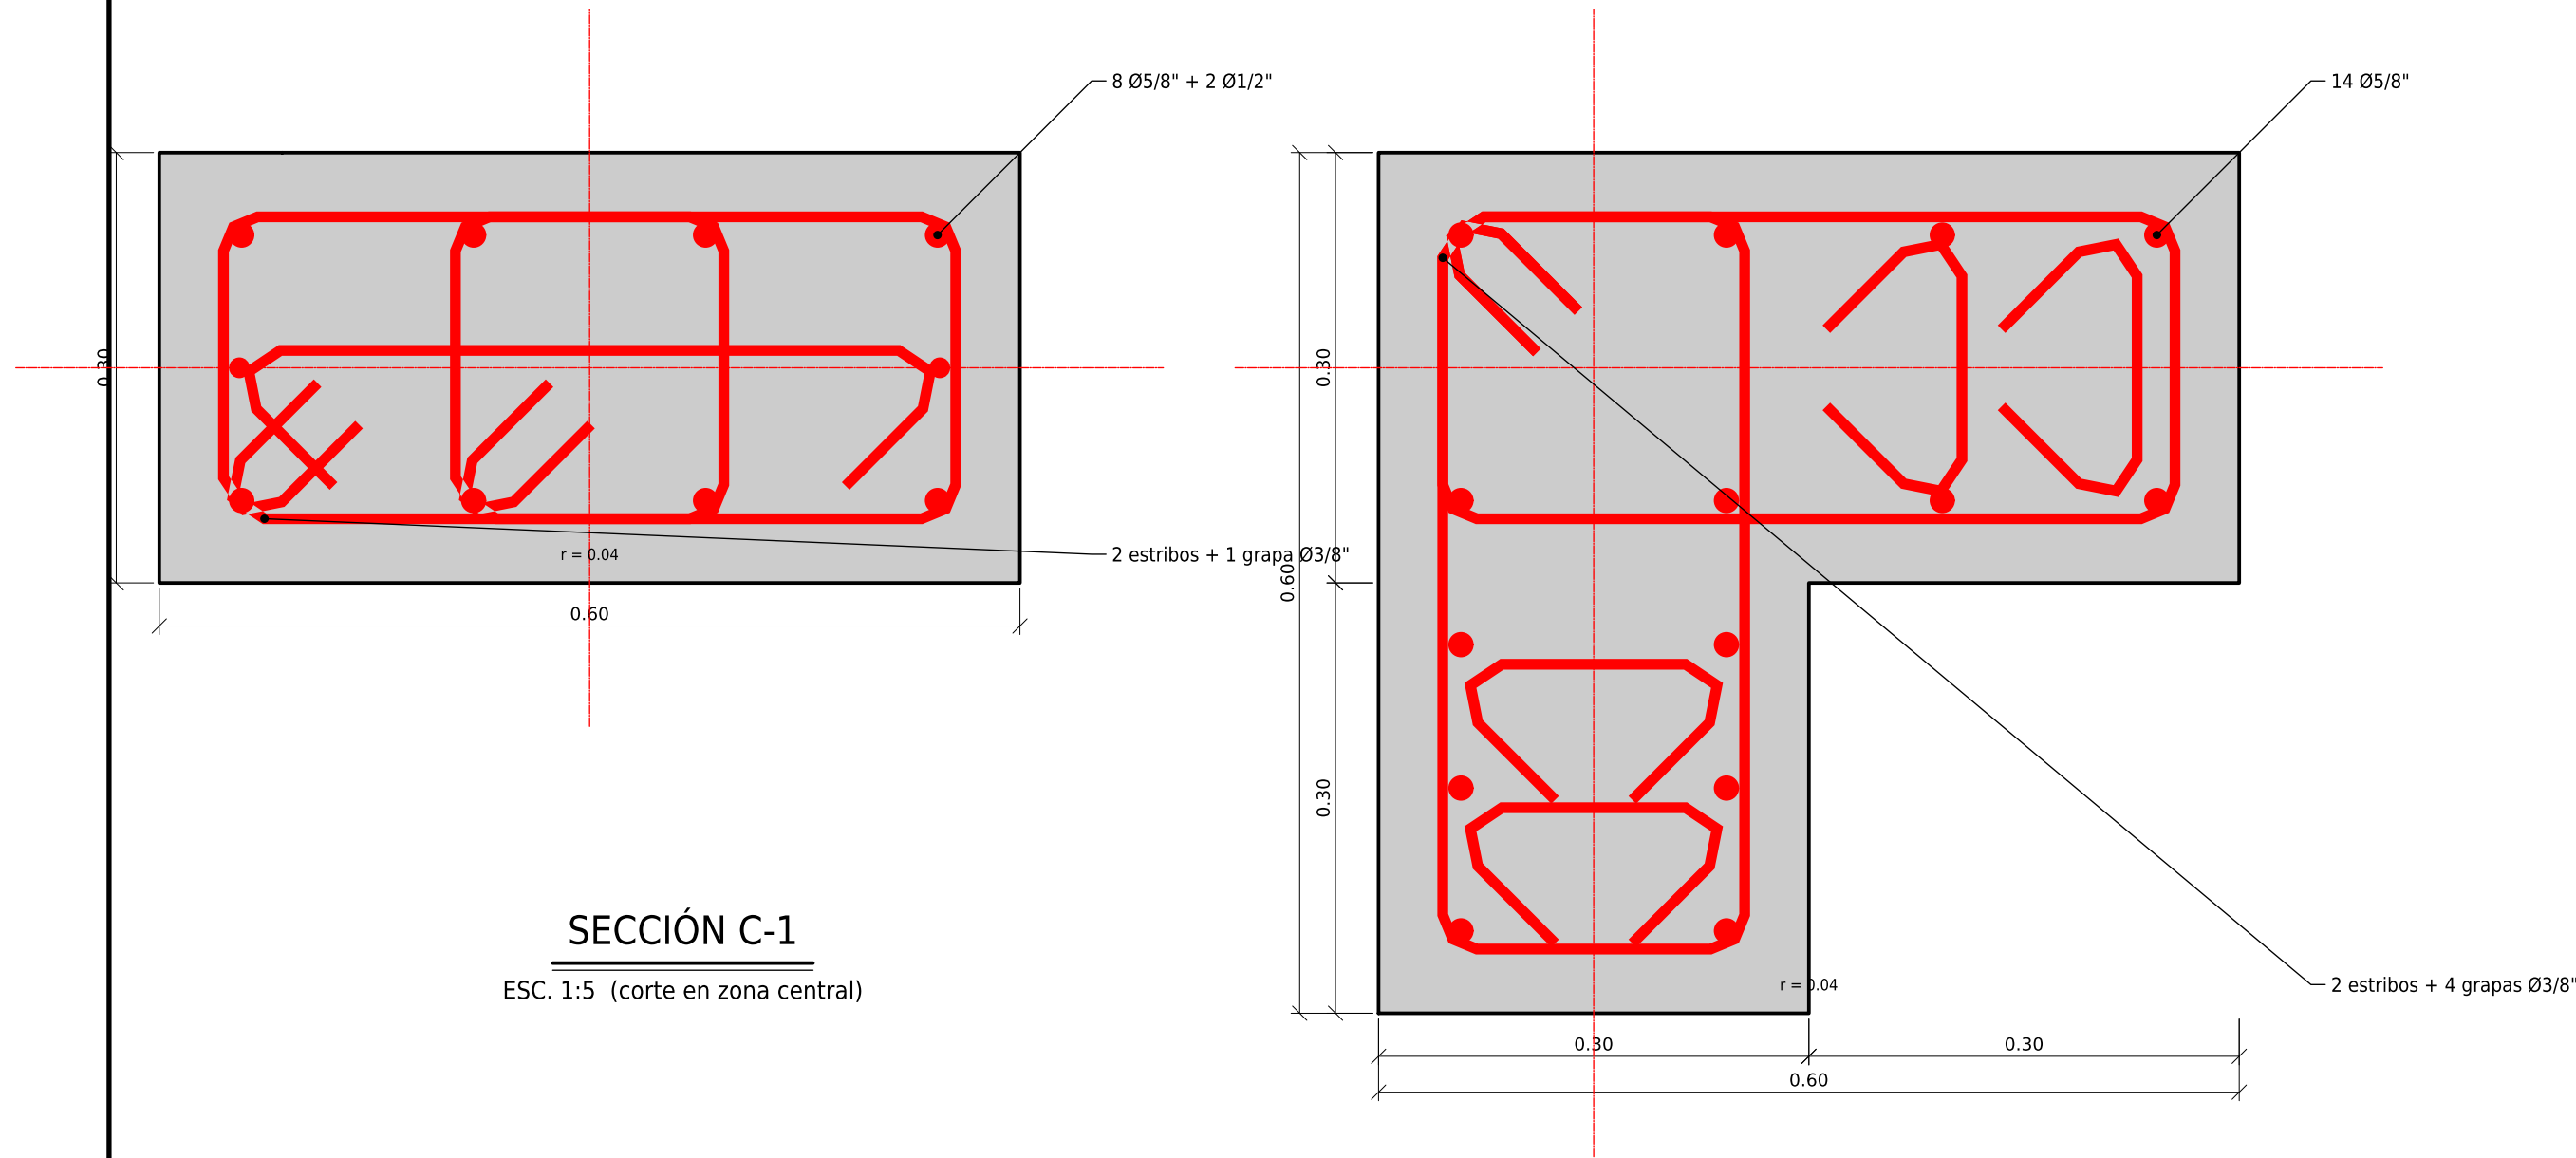

SECCIÓN C-1
ESC. 1:5 (corte en zona central)

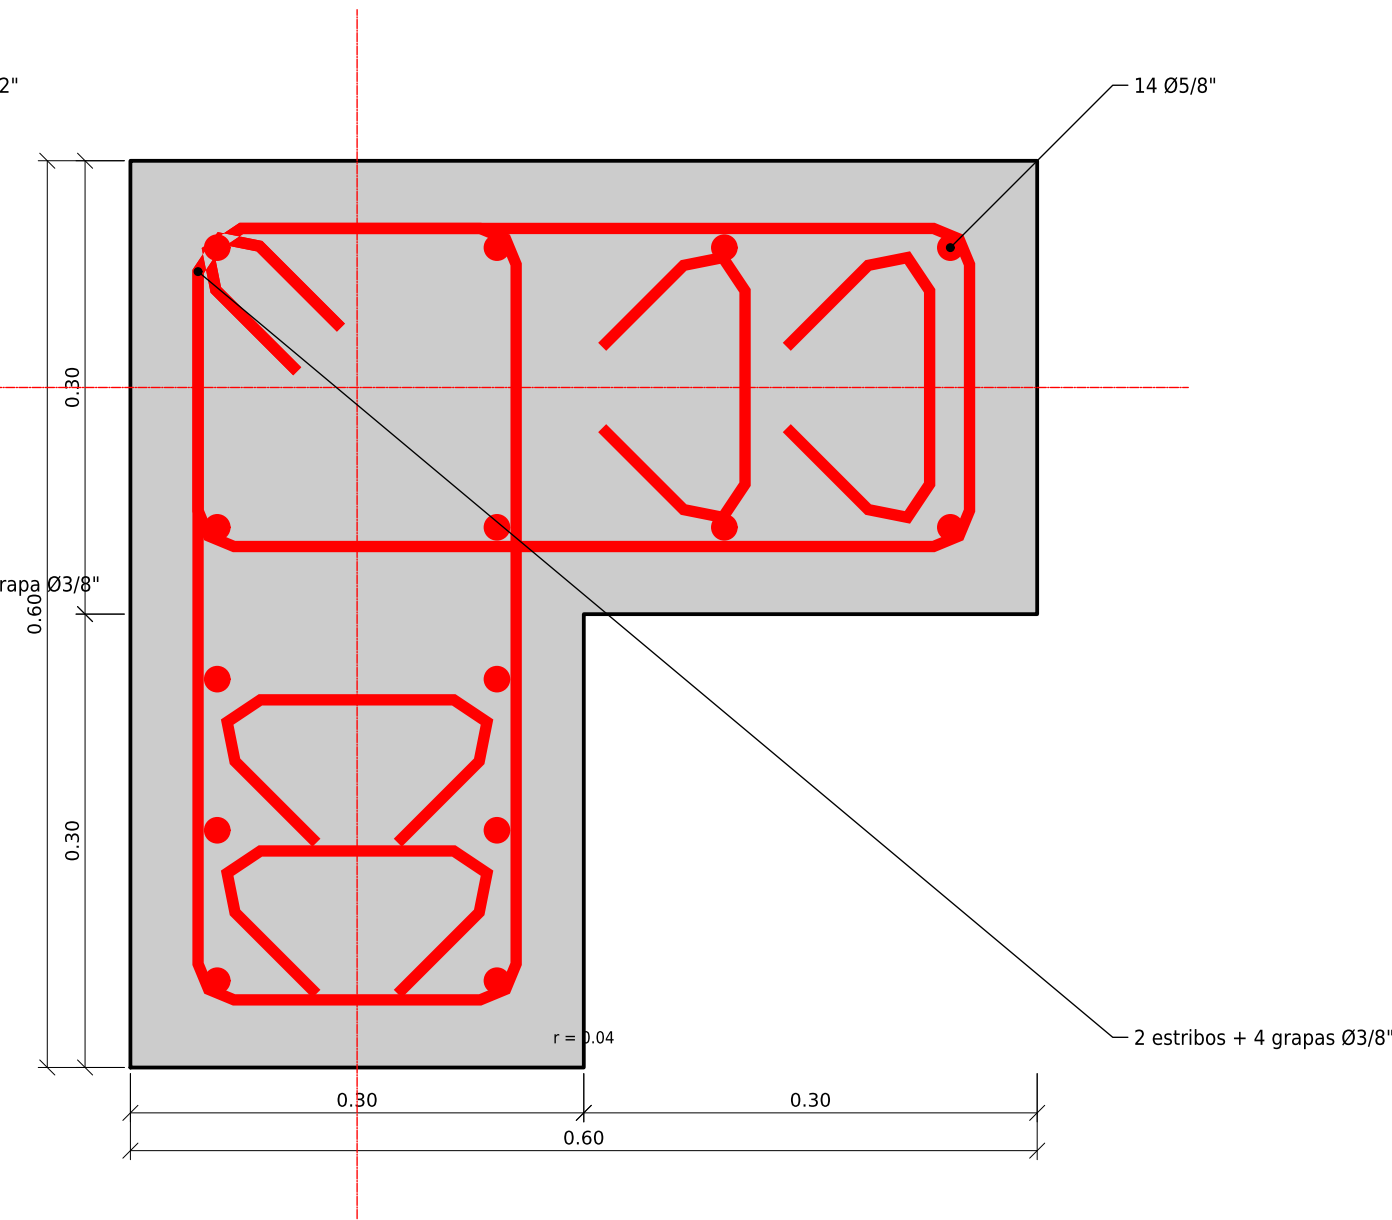


SECCIÓN C-2
ESC. 1:5 (corte en zona central)


CUADRO DE COLUMNAS (medido del modelo)

TRAMO	C-1 0.60 x 0.30 (10 + 2 escalera)	C-2 L 0.60 x 0.60 x 0.30 (4)
Cimentación - Nivel 1	todo @ .10	todo @ .10
Nivel 1 - Nivel 2	1@.05, 6@.10, 2@.15, rto. @.20 c/ext.; @.10 en traslape	1@.05, 6@.10, 2@.15, rto. @.20 c/ext.; @.10 en traslape
Nivel 2 - Nivel 3	1@.05, 6@.10, 2@.15, rto. @.20 c/ext.; @.10 en traslape	1@.05, 6@.10, 2@.15, rto. @.20 c/ext.; @.10 en traslape
Nivel 3 - Nivel 4	1@.05, 6@.10, 2@.15, rto. @.20 c/ext.; @.10 en traslape	1@.05, 6@.10, 2@.15, rto. @.20 c/ext.; @.10 en traslape
Nivel 4 - Nivel 5	1@.05, 6@.10, 2@.15, rto. @.20 c/ext.; @.10 en traslape	1@.05, 6@.10, 2@.15, rto. @.20 c/ext.; @.10 en traslape
LONGITUDINAL	8 Ø5/8" + 2 Ø1/2"	14 Ø5/8"
ESTRIBOS	2 estribos + 1 grapa Ø3/8" por juego	2 estribos + 4 grapas Ø3/8" por juego


- NOTAS - COLUMNAS
- CONCRETO $f_c = 210 \text{ kg/cm}^2$. ACERO ASTM A615 Gr. 60, $f_y = 4200 \text{ kg/cm}^2$.
 - RECUBRIMIENTO libre al estribo 4 cm.
 - Estribos cerrados con ganchos de 135° y extensión 6 db ($\geq 7.5 \text{ cm}$); grapas con 135°/90° alternados.
 - Traslapes clase B a media altura libre: Ø5/8" 0.75 m, Ø1/2" 0.60 m, con bayoneta 1:6.
 - Arranques: ver E-01 (pata 12 db sobre la parrilla). Remate en el techo: doblez 90° hacia el núcleo.
 - Distribución de estribos tomada de los conjuntos del modelo (zonas CONF / CENTRAL / TRASLAPE).
 - Columnas de escalera (ESQUINA_A2, ESQUINA_A3) armadas como C-1.

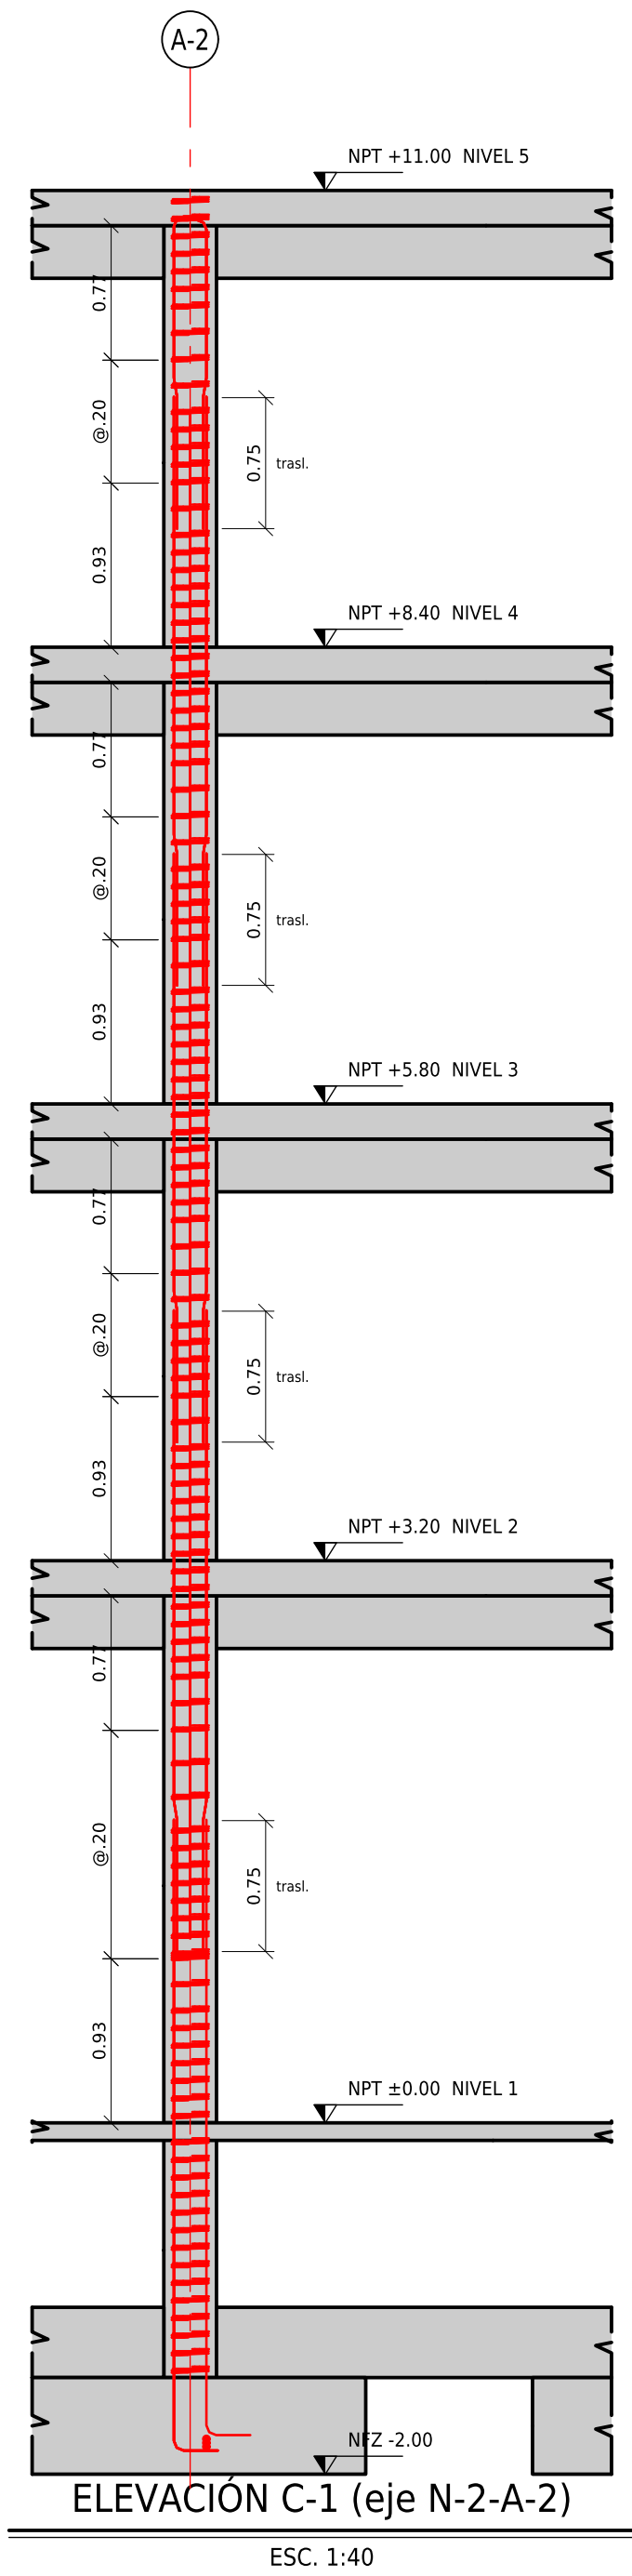


ELEVACIÓN C-1 (eje N-2-A-2)
ESC. 1:40

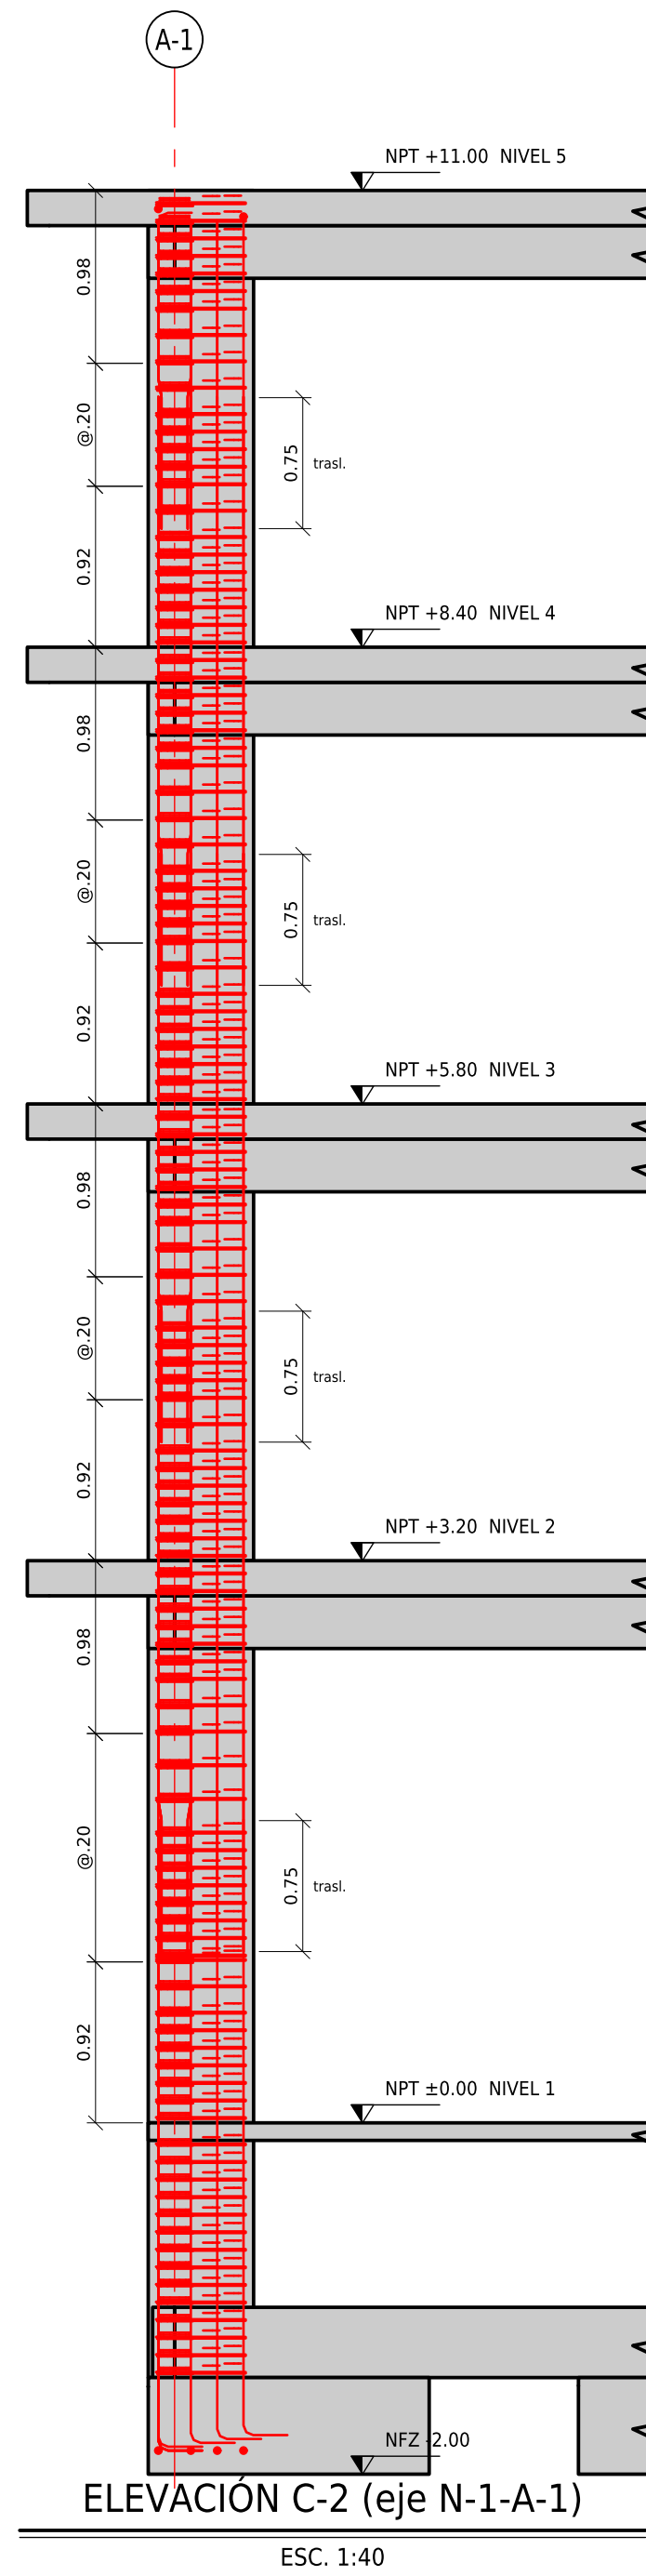

ELEVACIÓN C-2 (eje N-1-A-1)
ESC. 1:40

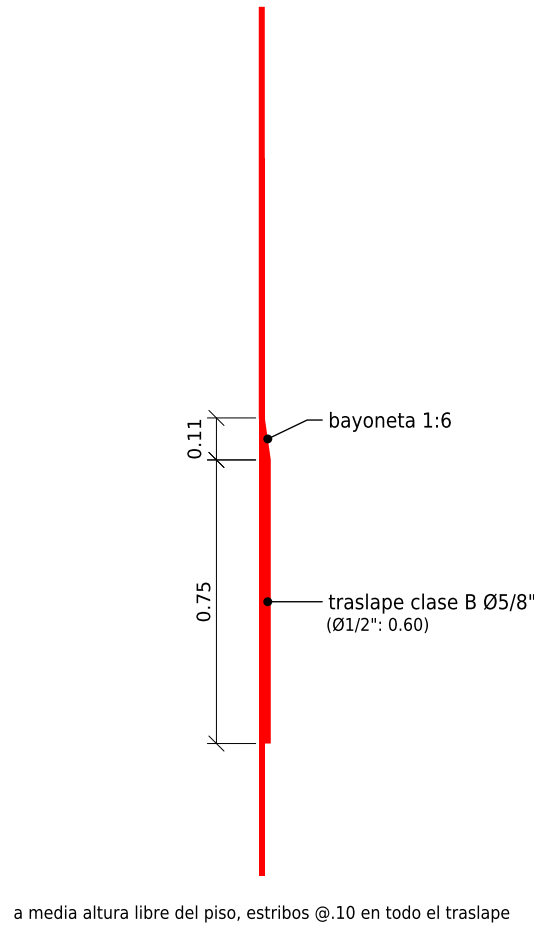

DETALLE DE TRASLAPE
ESC. 1:20

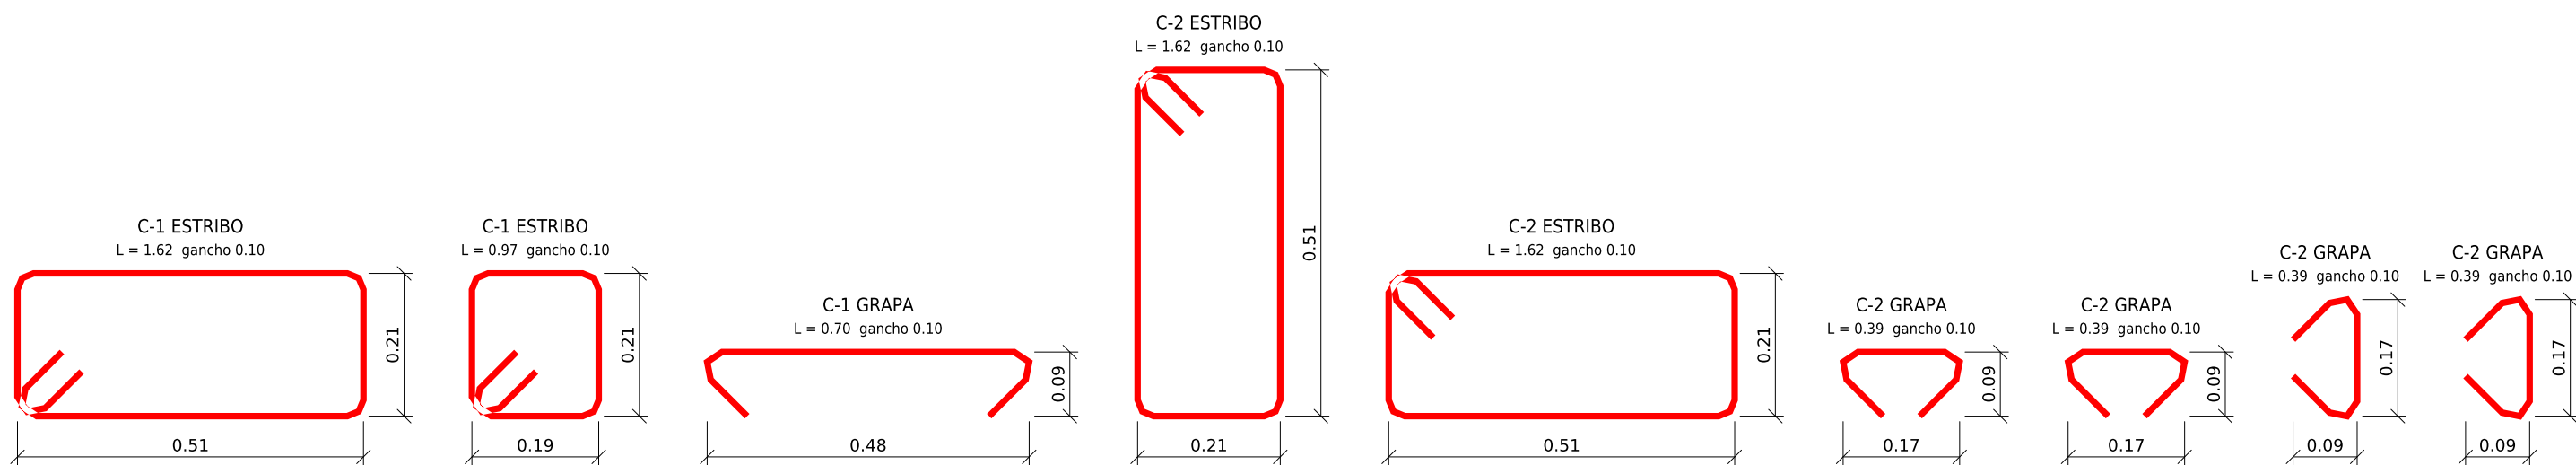

DETALLE DE ESTRIBOS Y GRAPAS (juego típico, medidas exteriores del modelo)
ESC. 1:10

PROYECTO:
CASA SAN JERÓNIMO - REDISEÑO ESTRUCTURAL 4 x 3
5 niveles (Cimentación -2.00, N1 ±0.00 ... N5 +11.00)

ESPECIALIDAD: ESTRUCTURAS
COLUMNAS: SECCIONES, ELEVACIONES
Y CUADRO DE COLUMNAS

ESCALA: INDICADA
FECHA: SET. 2026

FUENTE: modelo IFC 'Project sj.ifc'
(Revit 2027, IFC4, 26-09-2026)

PROFESIONAL RESPONSABLE:
CIP _____

REVISÓ:

LÁMINA
E-03