


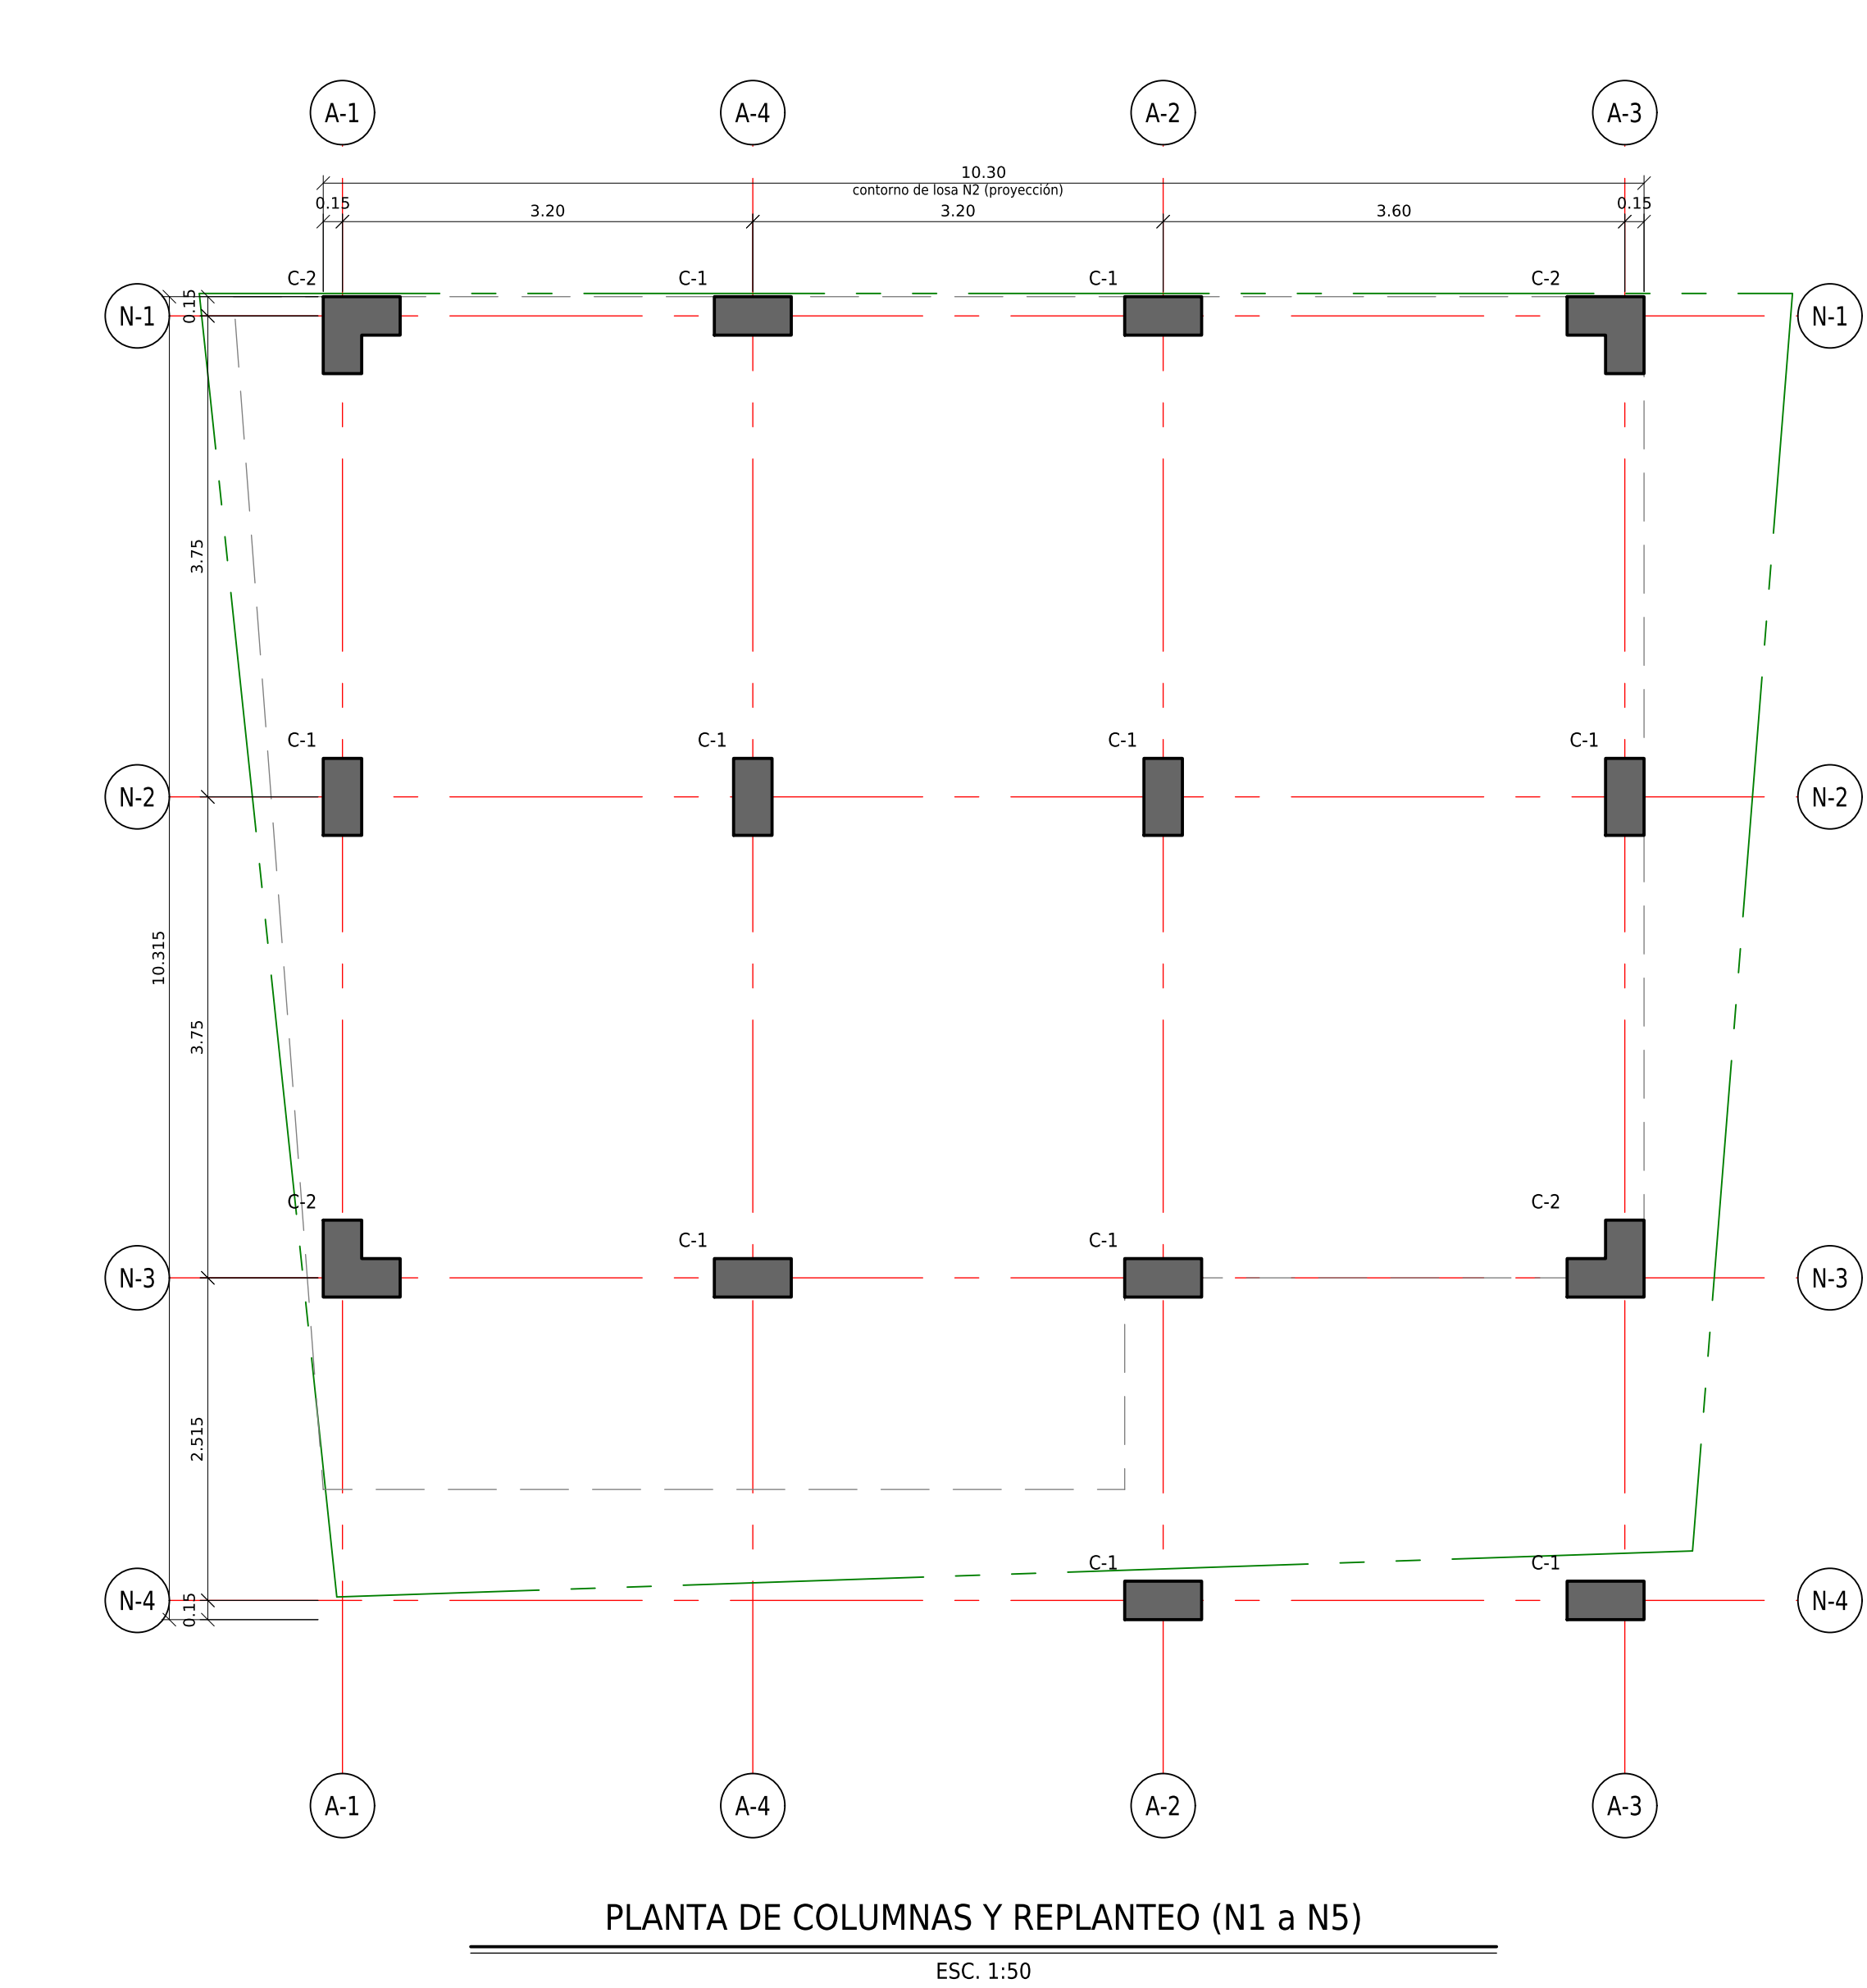

CUADRO DE COLUMNAS POR TIPO (armado: ver E-03)


TIPO	SECCIÓN	CANT./NIVEL	UBICACIÓN
C-1	0.60 x 0.30 (0.30 x 0.60 girada)	10	ESQUINA_A2, ESQUINA_A3, N-1/A-2, N-1/A-4, N-2/A-1, N-2/A-2, N-2/A-3, N-2/A-4, N-3/A-2, N-3/A-4
C-2	L 0.60 x 0.60, alas 0.30	4	N-1/A-1, N-1/A-3, N-3/A-1, N-3/A-3

CUADRO DE NIVELES

NIVEL	COTA (m)	ALTURA ENTREPISO (m)
Fondo de cimentación	-2.00	2.00
Nivel 1	+0.00	3.20
Nivel 2	+3.20	2.60
Nivel 3	+5.80	2.60
Nivel 4	+8.40	2.60
Nivel 5	+11.00	—


NOTAS

- Replanteo según cuadro (caras de cada columna a sus ejes, en metros). Columnas iguales en todos los niveles.
- Ejes según modelo: el orden en planta es A-1, A-4, A-2, A-3 (no correlativo).
- Columnas de escalera (eje N-4) sobre zapatas Z-1; ver E-01 y E-09.
- Límite de propiedad según modelo; las zapatas y columnas de N-4 lo sobrepasan: verificar con el levantamiento.

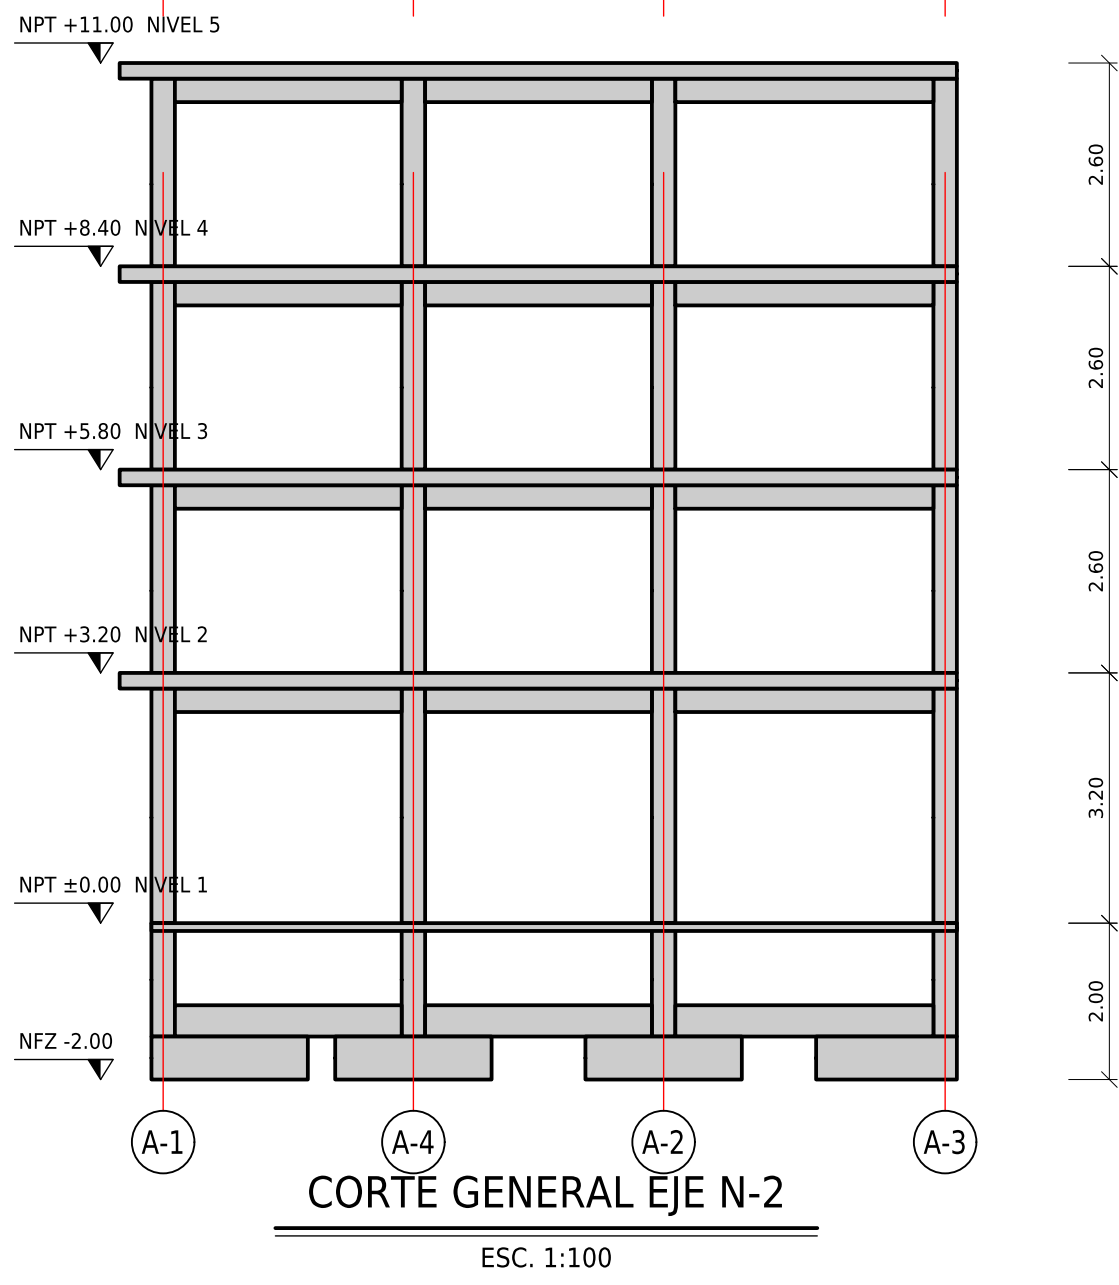

CORTE GENERAL EJE N-2

ESC. 1:100

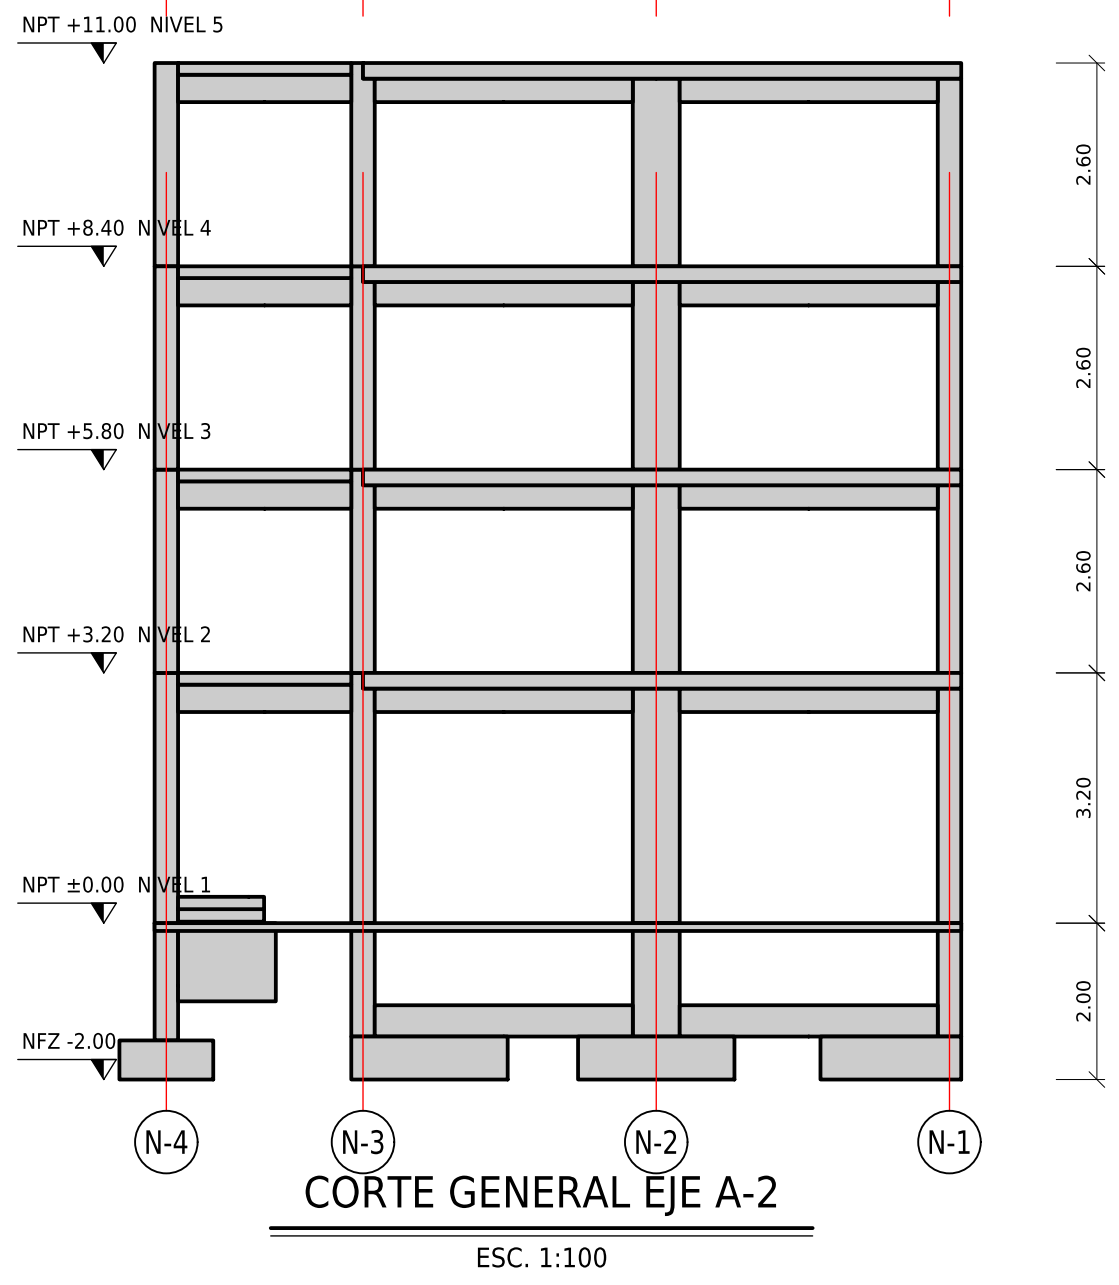

CORTE GENERAL EJE A-2

ESC. 1:100

CUADRO DE REPLANTEO: distancia de cada cara al eje (m)

COLUMNA	TIPO	EJES	IZQ. (-X)	DER. (+X)	ABAJO (-Y)	ARRIBA (+Y)
N-1/A-1	C-2	A-1 / N-1	0.15	0.45	0.45	0.15
N-1/A-4	C-1	A-4 / N-1	0.30	0.30	0.15	0.15
N-1/A-2	C-1	A-2 / N-1	0.30	0.30	0.15	0.15
N-1/A-3	C-2	A-3 / N-1	0.45	0.15	0.45	0.15
N-2/A-1	C-1	A-1 / N-2	0.15	0.15	0.30	0.30
N-2/A-4	C-1	A-4 / N-2	0.15	0.15	0.30	0.30
N-2/A-2	C-1	A-2 / N-2	0.15	0.15	0.30	0.30
N-2/A-3	C-1	A-3 / N-2	0.15	0.15	0.30	0.30
N-3/A-1	C-2	A-1 / N-3	0.15	0.45	0.15	0.45
N-3/A-4	C-1	A-4 / N-3	0.30	0.30	0.15	0.15
N-3/A-2	C-1	A-2 / N-3	0.30	0.30	0.15	0.15
N-3/A-3	C-2	A-3 / N-3	0.45	0.15	0.15	0.45
ESQUINA_A2	C-1	A-2 / N-4	0.30	0.30	0.15	0.15
ESQUINA_A3	C-1	A-3 / N-4	0.45	0.15	0.15	0.15

X a lo largo de los ejes N (hacia A-3); Y a lo largo de los ejes A (hacia N-1).

PROYECTO:

CASA SAN JERÓNIMO - REDISEÑO ESTRUCTURAL 4 x 3

5 niveles (Cimentación -2.00, N1 ±0.00 ... N5 +11.00)

ESPECIALIDAD: ESTRUCTURAS
PLANTA DE COLUMNAS (REPLANTEO)
Y CORTES GENERALES

ESCALA: INDICADA

FECHA: SET. 2026

FUENTE: modelo IFC 'Proyect sj.ifc'

(Revit 2027, IFC4, 26-09-2026)

PROFESIONAL RESPONSABLE:

CIP

REVISÓ:

LÁMINA

E-02