


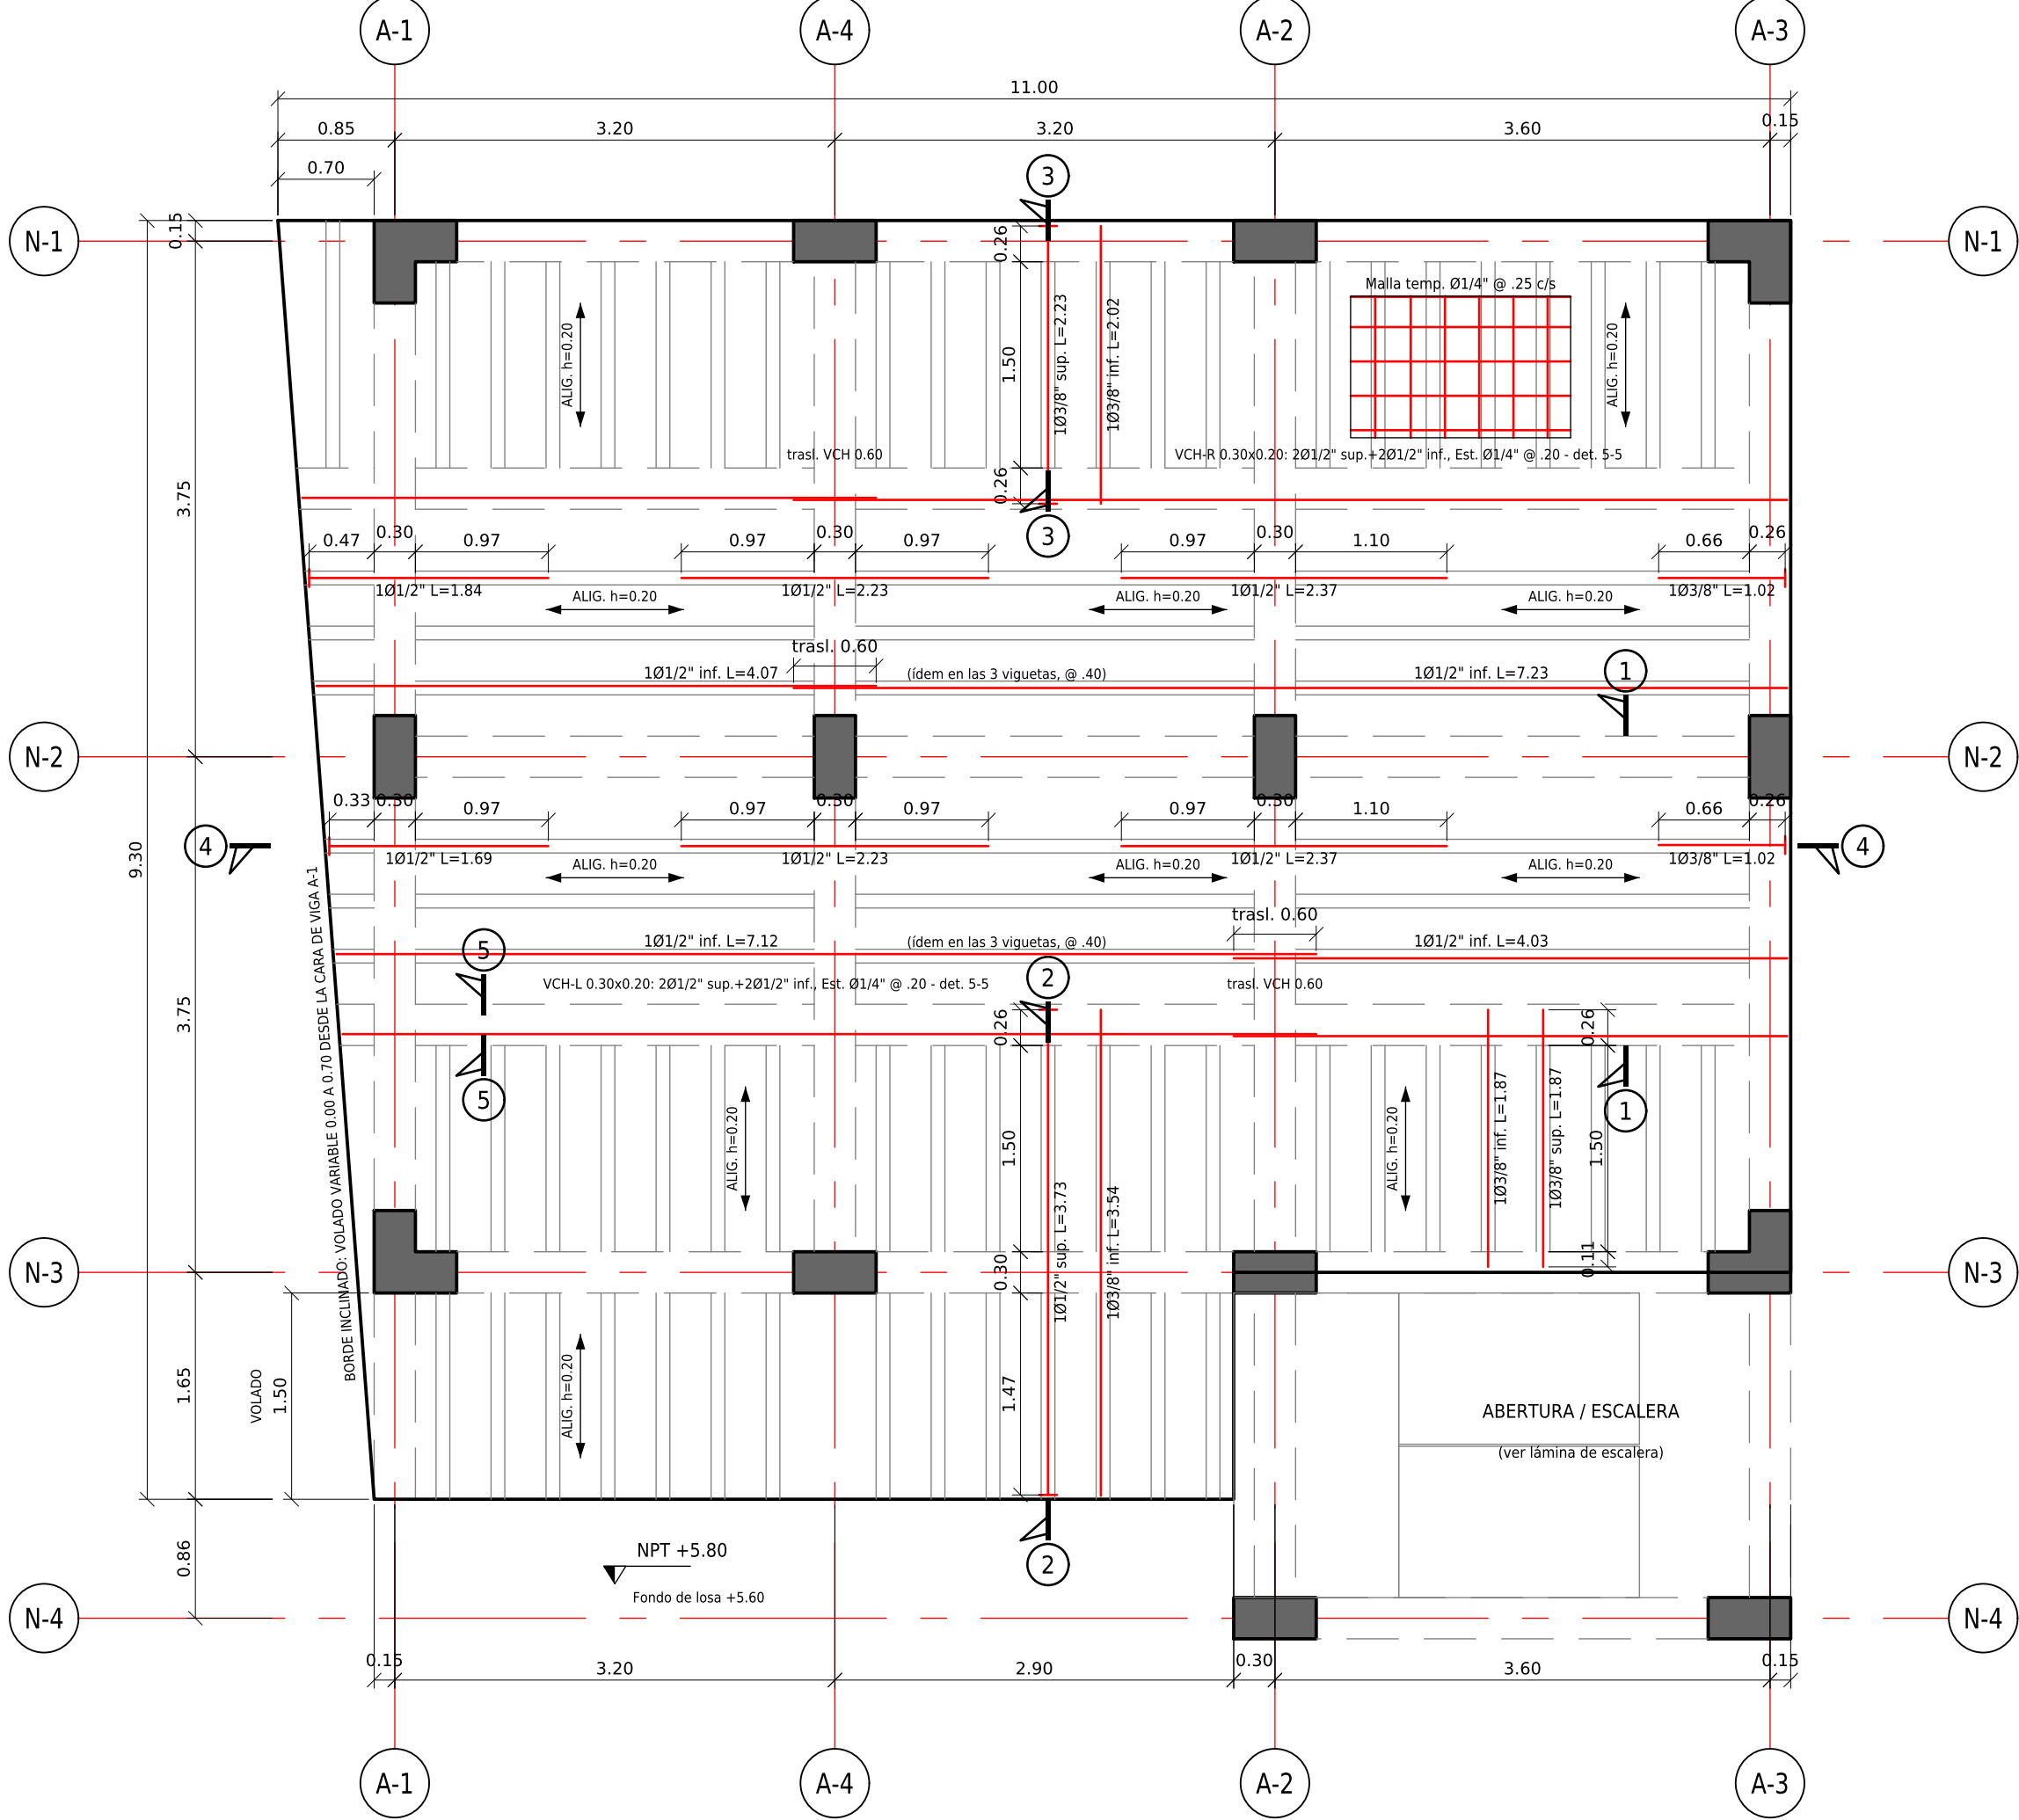


PLANTA DE LOSA ALIGERADA - NIVEL 3 (NPT +5.80)

ESC. 1:50


MARCA	DESCRIPCIÓN	Ø	CANT.	L UNIT. (m)	L TOTAL (m)	PESO (kg)
V1	Vigueta dir. X: inferior corrido (trasl. 0.60 sobre viga interior)	Ø1/2"	12	4.03 - 7.23	67.51	67.1
B1	Vigueta dir. X: bastón superior sobre apoyos interiores A-4 / A-2	Ø1/2"	12	2.23 - 2.37	27.60	27.4
B2	Vigueta dir. X: bastón superior apoyo extremo A-3 (gancho)	Ø3/8"	6	1.02	6.12	3.4
B3	Vigueta dir. X: superior del volado eje A-1 (gancho en borde)	Ø1/2"	6	1.63 - 1.84	10.39	10.3
L1	Vigueta dir. Y volado N-4: superior, borde a VCH (ganchos)	Ø1/2"	14	3.73	52.23	51.9
L2	Vigueta dir. Y lado escalera: superior, borde a VCH	Ø3/8"	8	1.87	14.96	8.4
L3	Vigueta dir. Y borde N-1: superior, viga N-1 a VCH (ganchos)	Ø3/8"	23	2.02 - 2.23	51.11	28.6
L4	Vigueta dir. Y (lado N-4 / N-3): inferior constructivo	Ø3/8"	22	1.87 - 3.54	64.45	36.1
L5	Vigueta dir. Y (lado N-1): inferior constructivo	Ø3/8"	23	2.02	46.46	26.0
C1	Viga chata VCH 0.30x0.20: superior 2 barras corridas	Ø1/2"	8	4.03 - 7.23	45.03	44.8
C2	Viga chata VCH 0.30x0.20: inferior 2 barras corridas	Ø1/2"	8	4.03 - 7.23	45.03	44.8
C3	Viga chata VCH: estribos 0.25 x 0.12 @ .20	Ø1/4"	90	0.86	77.08	19.3
T1	Maila de temperatura en losita, dir. X	Ø1/4"	69	3.88 - 7.08	383.77	95.9
T2	Maila de temperatura en losita, dir. Y	Ø1/4"	69	3.59 - 7.60	378.43	94.6
TOTAL Ø1/4" (0.250 kg/m)						209.8
TOTAL Ø3/8" (0.560 kg/m)						102.5
TOTAL Ø1/2" (0.994 kg/m)						246.3
TOTAL ACERO DE LOSA DEL NIVEL						538.7
Área de losa (modelo) 92.36 m² -> cuantía						6.05 kg/m²

- NOTAS - LOSA ALIGERADA
- CONCRETO FC = kg/cm² (COMPLETAR). ACERO ASTM A615 Grado 60, fy = 4200 kg/cm².
 - ALIGERADO h = 0.20 en una dirección: viguetas 0.10 @ 0.40, losita 0.05, casetones de poliestireno 0.30 x 0.15. Los CASETONES NO ESTÁN MODELADOS: el modelo representa la losa como piso macizo de 0.20 (tipo PISO ESTRUCTURAL MACIZO, 200mm VOLADO); ubicarlos según la posición de viguetas de esta planta.
 - RECUBRIMIENTO libre 2 cm (medido: inferior 2.5 cm, superior 2.5 cm).
 - Viguetas de los paños en dir. X (paralelas a ejes N) apoyadas en las vigas de los ejes A. En las franjas laterales (volado lado N-4 y borde N-1) viguetas en dir. Y ancladas 1.50 m en la viga chata VCH 0.30x0.20.
 - Bastones: longitudes medidas desde la cara de apoyo. Barras > 9 m traslapadas 0.60 sobre la viga interior. Ganchos a 90° de 0.12 en bordes libres y apoyos extremos.
 - Maila de temperatura Ø1/4" en ambos sentidos en toda la losita (38 + 44 líneas, sep. medida 0.250 / 0.249 m).
 - Cargas de diseño (nodo Dynamo 14, Anexo A): piso terminado 100, tabiquería equivalente 210, s/c 200 kg/m²; muro de ladrillo de 10 cm en contorno y volados 516 kg/m.
 - Acero dibujado en planta: una vigueta representativa por franja (idem en todas las de la franja).
 - Plano generado del modelo IFC 'Project s.j.f.c' (Revit 2022); cotas y niveles en metros.

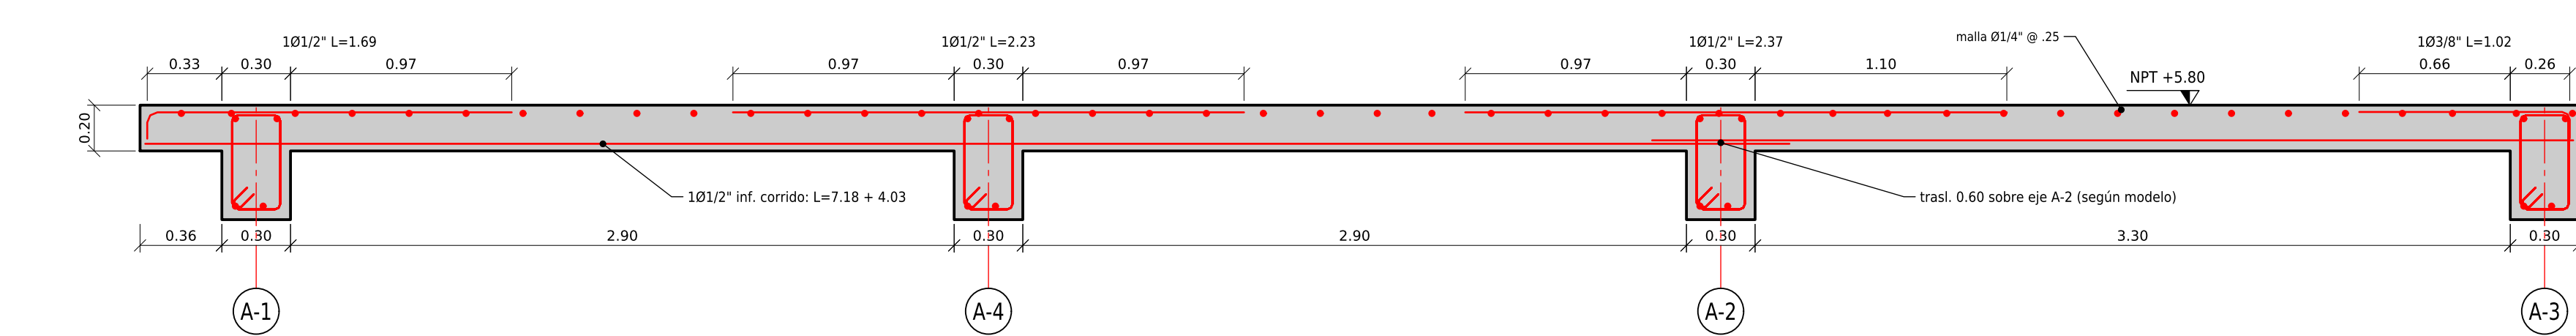


CORTE 4-4 LONGITUDINAL DE VIGUETA (dir. X)

ESC. 1:25 (vigueta en eje de 5.615 m; cotas de bastones desde la cara de apoyo)

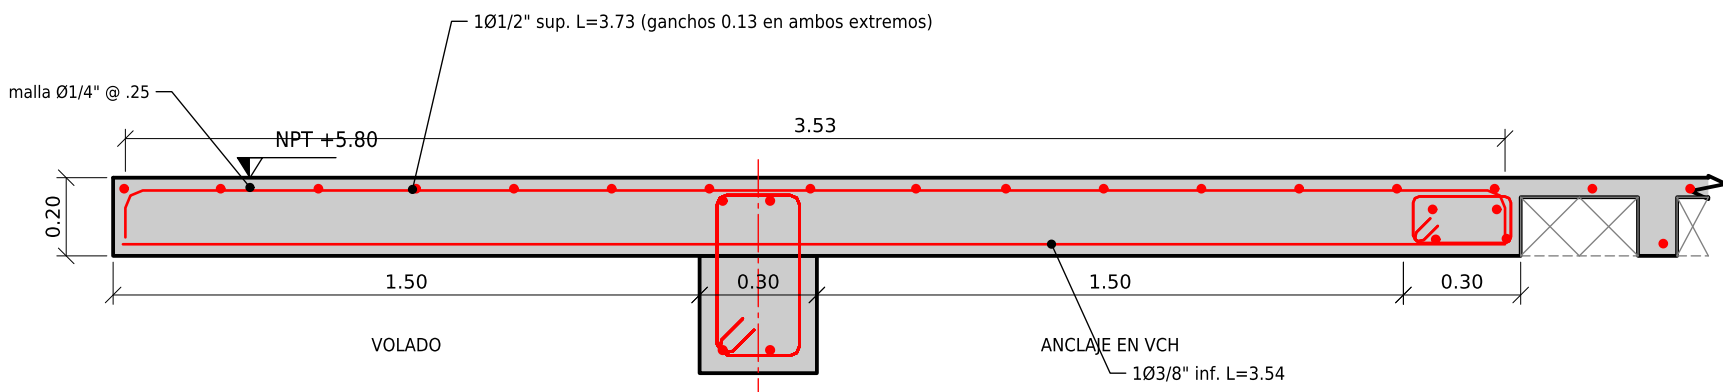


CORTE 2-2 VOLADO LADO N-4 Y VCH

ESC. 1:20

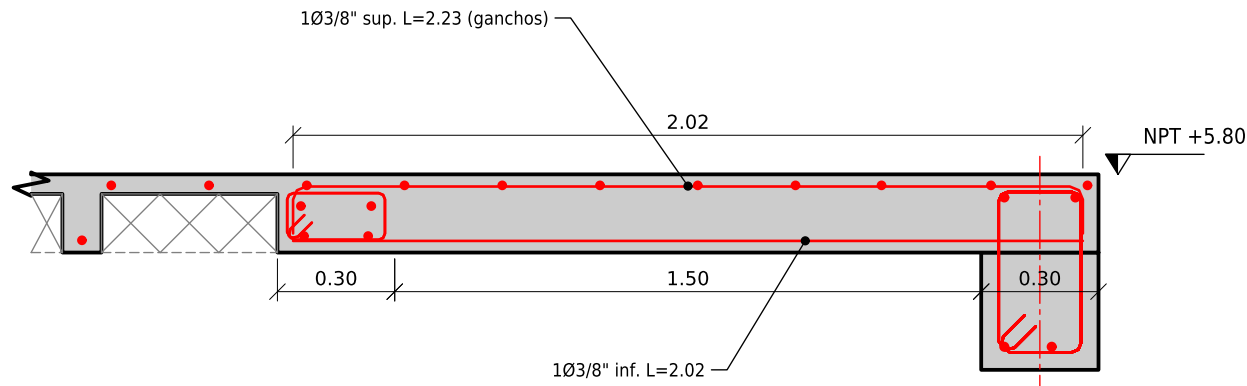


CORTE 3-3 BORDE N-1 Y VCH

ESC. 1:20

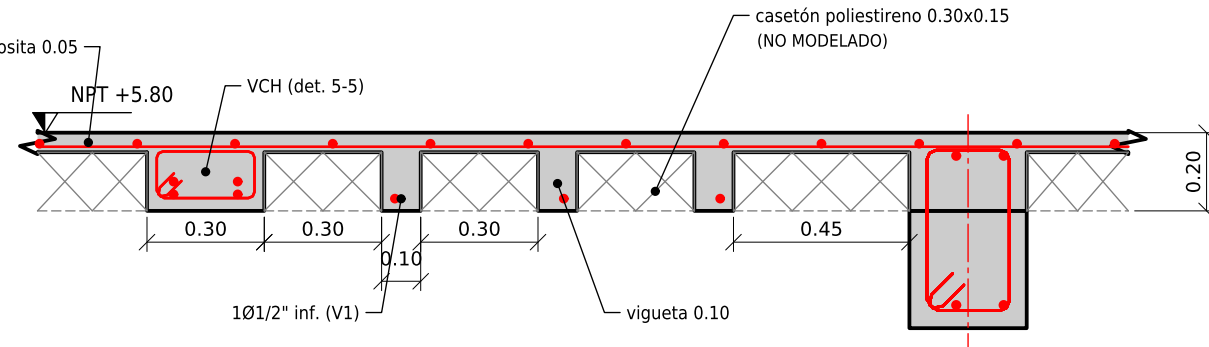

CORTE 1-1 ALIGERADO TÍPICO

ESC. 1:20

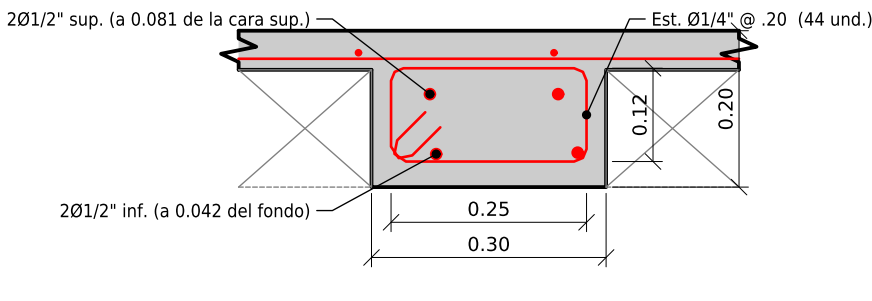

DETALLE 5-5 VIGA CHATA VCH

ESC. 1:10

CUADRO DE BASTONES Y ACERO SUPERIOR (tramos medidos del modelo, desde el extremo de la barra)

MARCA	Ø	UBICACIÓN	TRAMOS MEDIDOS (m): libre + [apoyo] + libre	GANCHOS	CANT.
B1	Ø1/2"	vigueta X, sobre apoyo interior	0.97 + [A-4 0.30] + 0.97 ... 0.97 + [A-2 0.30] + 1.10	-	12
B2	Ø3/8"	vigueta X, apoyo extremo A-3	0.66 + [A-3 0.26]	1 x 0.12	6
B3	Ø1/2"	vigueta X, volado A-1	0.27 + [A-1 0.30] + 0.97 ... 0.47 + [A-1 0.30] + 0.97	1 x 0.12	6
L1	Ø1/2"	vigueta Y, volado N-4	1.47 + [N-3 0.30] + 1.50 + [VCH 0.26]	2 x 0.13	14
L2	Ø3/8"	vigueta Y, lado escalera	[N-3 0.11] + 1.50 + [VCH 0.26]	-	8
L3	Ø3/8"	vigueta Y, borde N-1	[VCH 0.26] + 1.50 + [N-1 0.26]	2 x 0.12	23

Varias barras de un grupo: se indican la menor y la mayor (bordes inclinados). Apoyo = viga (eje) o viga chata VCH.

LEYENDA

- Columna bajo el nivel (achurado)
- Viga bajo la losa / viga chata VCH (línea oculta)
- Vigueta 0.10 (nervio) - casetones entre viguetas
- Dirección de viguetas, aligerado h = 0.20
- Acero de refuerzo (rep.): trazo corto = gancho 90°
- Borde de losa

PROYECTO:
CASA SAN JERÓNIMO - REDISEÑO ESTRUCTURAL 4 x 3
5 niveles (Cimentación -2.00, N1 ±0.00 ... N5 +11.00)

ESPECIALIDAD: ESTRUCTURAS
LOSA ALIGERADA - NIVEL 3 (NPT +5.80)
PLANTA, CORTES, DETALLE VCH Y CUADRO DE ACERO

ESCALA: INDICADA
FECHA: SET. 2026

FUENTE: modelo IFC 'Project s.j.f.c' (Revit 2022, IFC4, 26-09-2026)

PROFESIONAL RESPONSABLE:
CIP

REVISÓ:

LÁMINA

E-05