


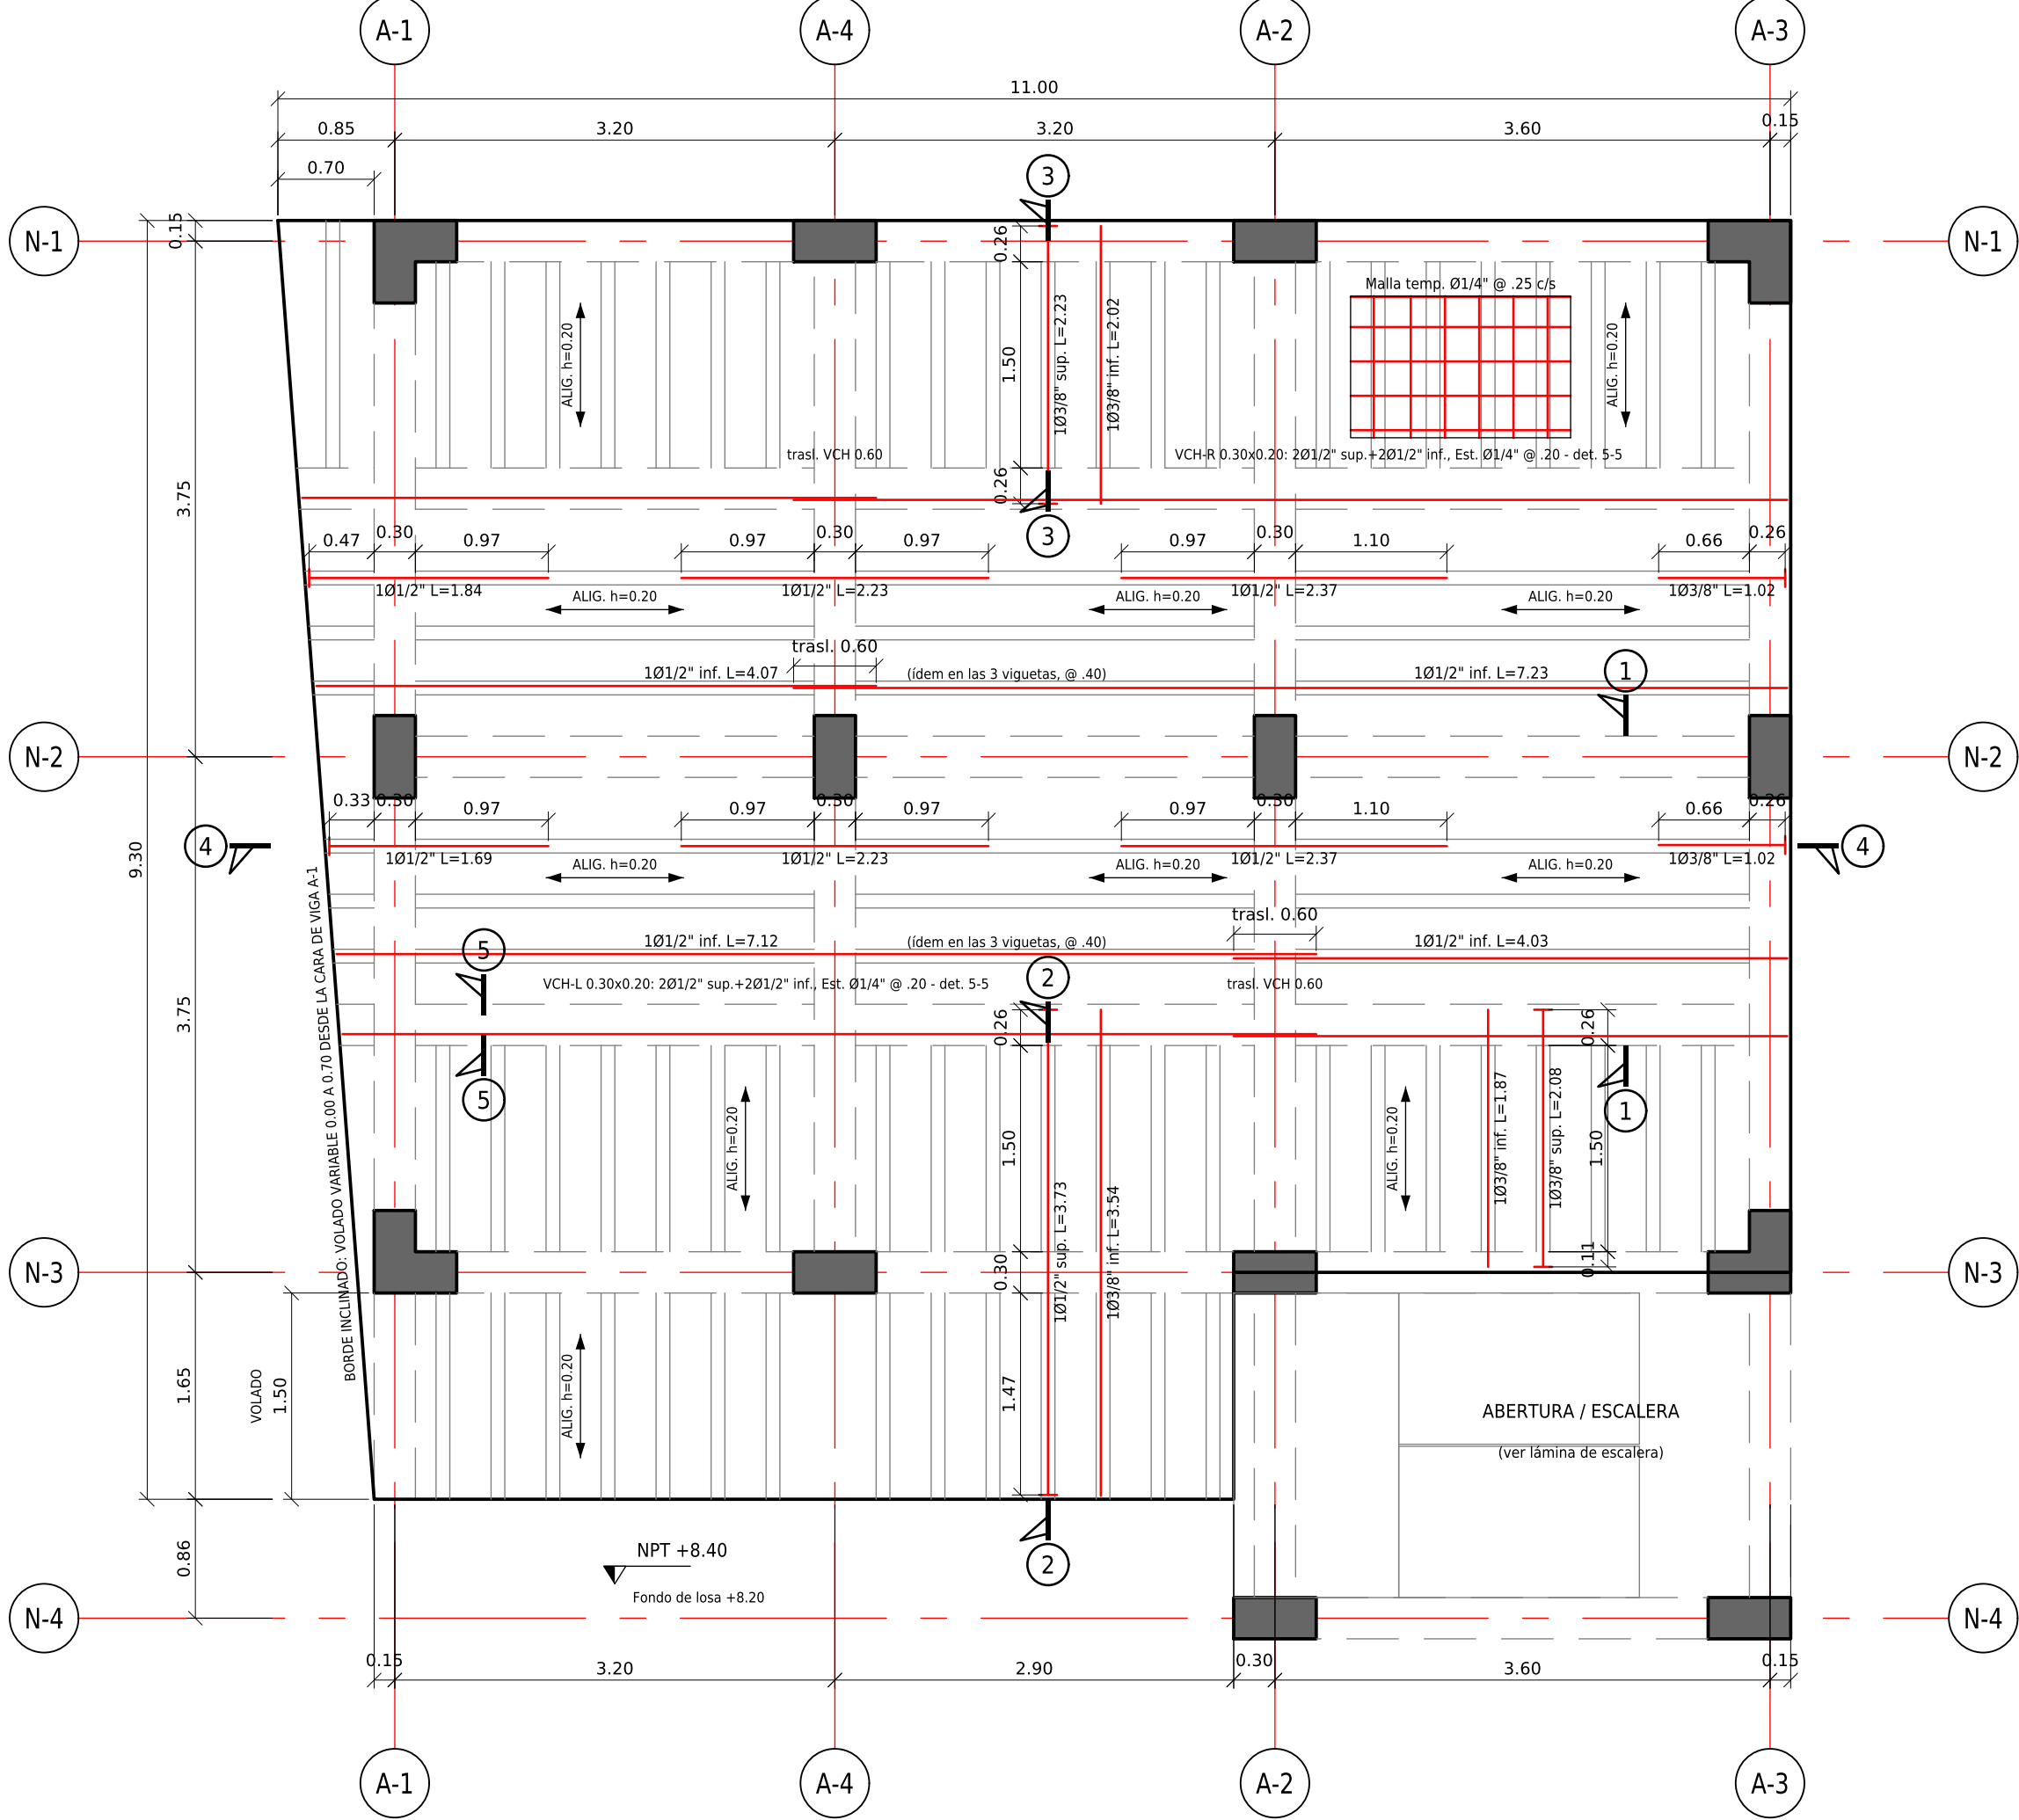


PLANTA DE LOSA ALIGERADA - NIVEL 4 (NPT +8.40)

ESC. 1:50


| MARCA                                     | DESCRIPCIÓN                                                        | Ø     | CANT. | L UNIT. (m) | L TOTAL (m) | PESO (kg)  |
|-------------------------------------------|--------------------------------------------------------------------|-------|-------|-------------|-------------|------------|
| V1                                        | Vigueta dir. X: inferior corrido (trasl. 0.60 sobre viga interior) | Ø1/2" | 12    | 4.03 - 7.23 | 67.51       | 67.1       |
| B1                                        | Vigueta dir. X: bastón superior sobre apoyos interiores A-4 / A-2  | Ø1/2" | 12    | 2.23 - 2.37 | 27.60       | 27.4       |
| B2                                        | Vigueta dir. X: bastón superior apoyo extremo A-3 (gancho)         | Ø3/8" | 6     | 1.02        | 6.12        | 3.4        |
| B3                                        | Vigueta dir. X: superior del volado eje A-1 (gancho en borde)      | Ø1/2" | 6     | 1.63 - 1.84 | 10.39       | 10.3       |
| L1                                        | Vigueta dir. Y volado N-4: superior, borde a VCH (ganchos)         | Ø1/2" | 14    | 3.73        | 52.23       | 51.9       |
| L2                                        | Vigueta dir. Y lado escalera: superior, borde a VCH                | Ø3/8" | 8     | 2.08        | 16.65       | 9.3        |
| L3                                        | Vigueta dir. Y borde N-1: superior, viga N-1 a VCH (ganchos)       | Ø3/8" | 23    | 2.02 - 2.23 | 51.11       | 28.6       |
| L4                                        | Vigueta dir. Y (lado N-4 / N-3): inferior constructivo             | Ø3/8" | 22    | 1.87 - 3.54 | 64.45       | 36.1       |
| L5                                        | Vigueta dir. Y (lado N-1): inferior constructivo                   | Ø3/8" | 23    | 2.02        | 46.46       | 26.0       |
| C1                                        | Viga chata VCH 0.30x0.20: superior 2 barras corridas               | Ø1/2" | 8     | 4.03 - 7.23 | 45.03       | 44.8       |
| C2                                        | Viga chata VCH 0.30x0.20: inferior 2 barras corridas               | Ø1/2" | 8     | 4.03 - 7.23 | 45.03       | 44.8       |
| C3                                        | Viga chata VCH: estribos 0.25 x 0.12 @ .20                         | Ø1/4" | 90    | 0.86        | 77.08       | 19.3       |
| T1                                        | Malla de temperatura en losita, dir. X                             | Ø1/4" | 69    | 3.88 - 7.08 | 383.77      | 95.9       |
| T2                                        | Malla de temperatura en losita, dir. Y                             | Ø1/4" | 69    | 3.59 - 7.60 | 378.43      | 94.6       |
| TOTAL Ø1/4" (0.250 kg/m)                  |                                                                    |       |       |             |             | 209.8      |
| TOTAL Ø3/8" (0.560 kg/m)                  |                                                                    |       |       |             |             | 103.5      |
| TOTAL Ø1/2" (0.994 kg/m)                  |                                                                    |       |       |             |             | 246.3      |
| TOTAL ACERO DE LOSA DEL NIVEL             |                                                                    |       |       |             |             | 559.6      |
| Área de losa (modelo) 92.36 m² -> cuantía |                                                                    |       |       |             |             | 6.06 kg/m² |

- NOTAS - LOSA ALIGERADA
- CONCRETO FC = kg/cm² (COMPLETAR). ACERO ASTM A615 Grado 60, fy = 4200 kg/cm².
  - ALIGERADO h = 0.20 en una dirección: viguetas 0.10 @ 0.40, losita 0.05, casetones de poliestireno 0.30 x 0.15. Los CASETONES NO ESTÁN MODELADOS: el modelo representa la losa como piso macizo de 0.20 (tipo PISO ESTRUCTURAL MACIZO, 200mm VOLADO); ubicarlos según la posición de viguetas de esta planta.
  - RECUBRIMIENTO libre 2 cm (medido: inferior 2.5 cm, superior 2.5 cm).
  - Viguetas de los paños en dir. X (paralelas a ejes N) apoyadas en las vigas de los ejes A. En las franjas laterales (volado lado N-4 y borde N-1) viguetas en dir. Y ancladas 1.50 m en la viga chata VCH 0.30x0.20.
  - Bastones: longitudes medidas desde la cara de apoyo. Barras > 9 m traslapadas 0.60 sobre la viga interior. Ganchos a 90° de 0.12 en bordes libres y apoyos extremos.
  - Malla de temperatura Ø1/4" en ambos sentidos en toda la losita (38 + 44 líneas, sep. medida 0.250 / 0.249 m).
  - Cargas de diseño (nodo Dynamo 14, Anexo A): piso terminado 100, tabiquería equivalente 210, s/c 200 kg/m²; muro de ladrillo de 10 cm en contorno y volados 516 kg/m.
  - Acero dibujado en planta: una vigueta representativa por franja (idem en todas las de la franja).
  - Plano generado del modelo IFC 'Project s.j.fc' (Revit 2022); cotas y niveles en metros.

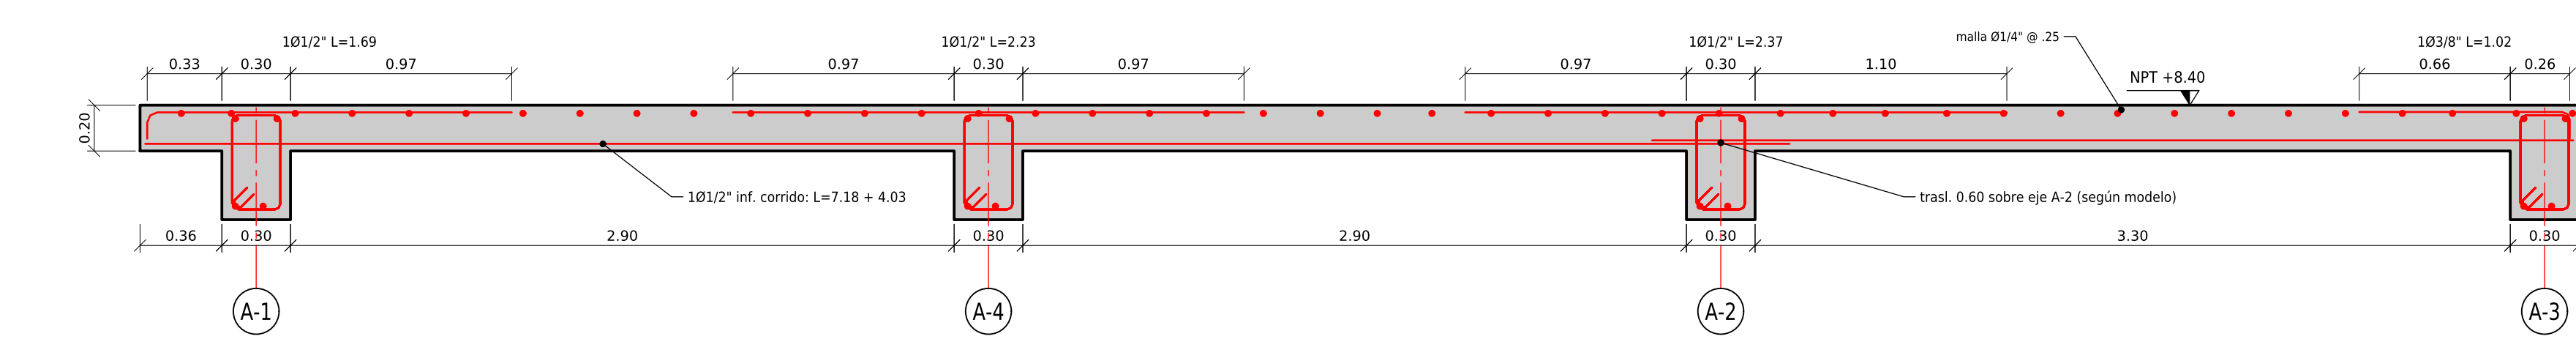


CORTE 4-4 LONGITUDINAL DE VIGUETA (dir. X)

ESC. 1:25 (vigueta en eje de 5.615 m; cotas de bastones desde la cara de apoyo)

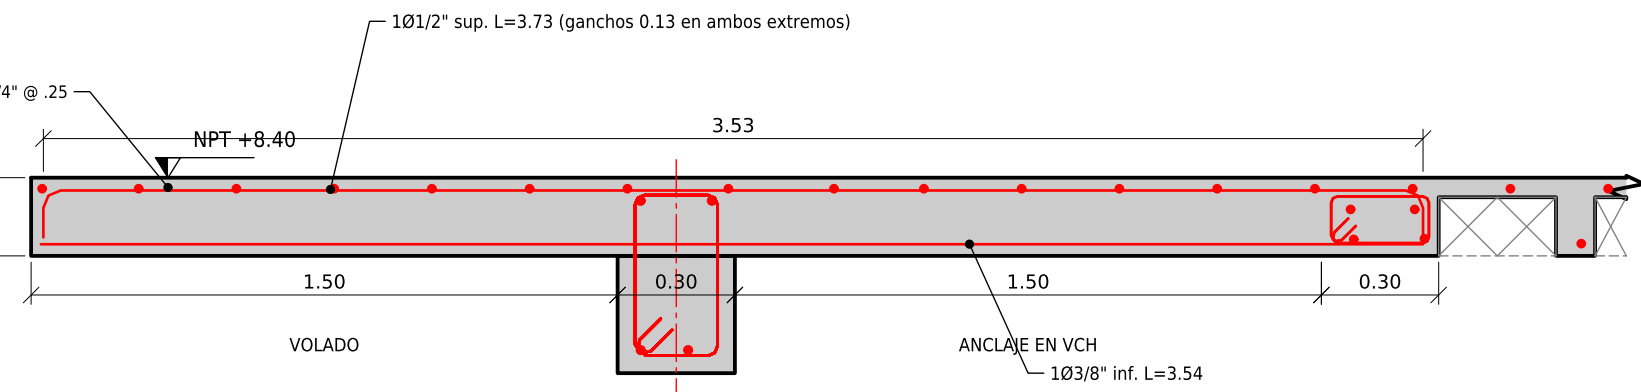


CORTE 2-2 VOLADO LADO N-4 Y VCH

ESC. 1:20

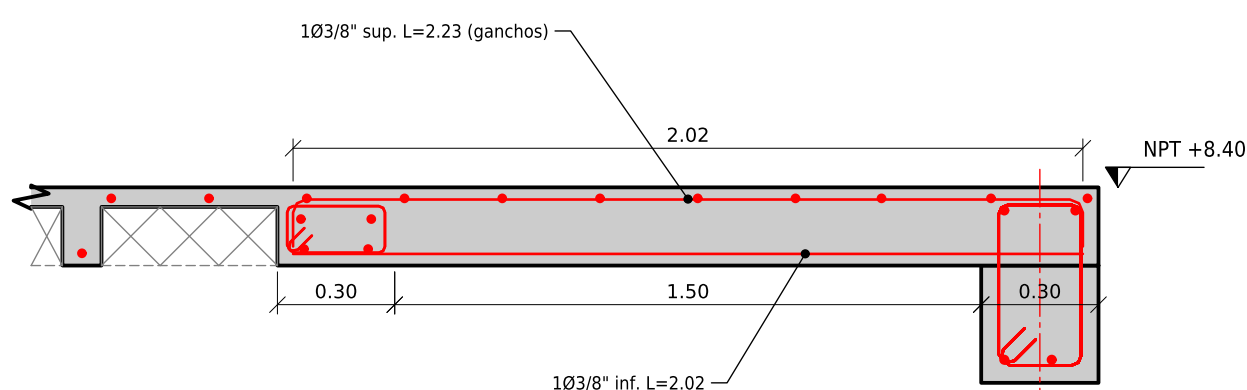


CORTE 3-3 BORDE N-1 Y VCH

ESC. 1:20

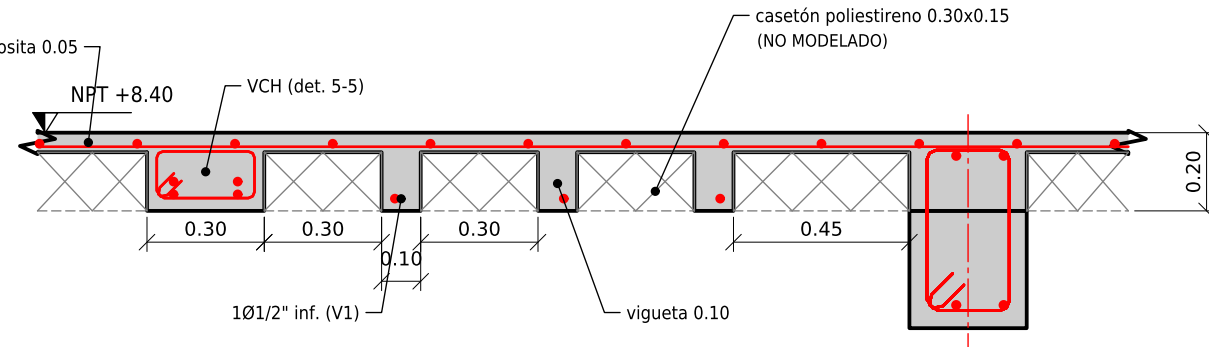

CORTE 1-1 ALIGERADO TÍPICO

ESC. 1:20

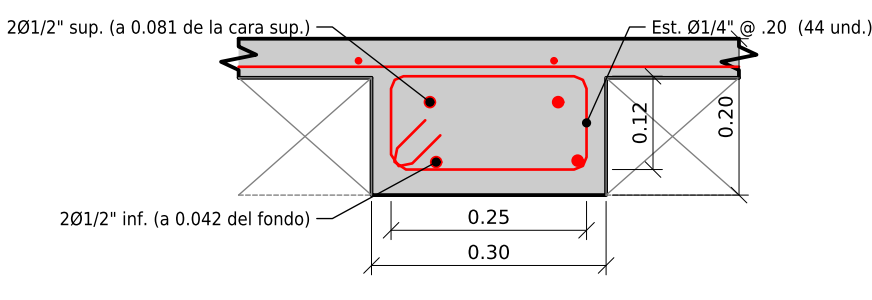

DETALLE 5-5 VIGA CHATA VCH

ESC. 1:10

| MARCA | Ø     | UBICACIÓN                       | TRAMOS MEDIDOS (m): libre + [apoyo] + libre           | GANCHOS  | CANT. |
|-------|-------|---------------------------------|-------------------------------------------------------|----------|-------|
| B1    | Ø1/2" | vigueta X, sobre apoyo interior | 0.97 + [A-4 0.30] + 0.97 ... 0.97 + [A-2 0.30] + 1.10 | -        | 12    |
| B2    | Ø3/8" | vigueta X, apoyo extremo A-3    | 0.66 + [A-3 0.26]                                     | 1 x 0.12 | 6     |
| B3    | Ø1/2" | vigueta X, volado A-1           | 0.27 + [A-1 0.30] + 0.97 ... 0.47 + [A-1 0.30] + 0.97 | 1 x 0.12 | 6     |
| L1    | Ø1/2" | vigueta Y, volado N-4           | 1.47 + [N-3 0.30] + 1.50 + [VCH 0.26]                 | 2 x 0.13 | 14    |
| L2    | Ø3/8" | vigueta Y, lado escalera        | [N-3 0.11] + 1.50 + [VCH 0.26]                        | 2 x 0.12 | 8     |
| L3    | Ø3/8" | vigueta Y, borde N-1            | [VCH 0.26] + 1.50 + [N-1 0.26]                        | 2 x 0.12 | 23    |

Varias barras de un grupo: se indican la menor y la mayor (bordes inclinados). Apoyo = viga (eje) o viga chata VCH.

- LEYENDA
- Columna bajo el nivel (achurado)
  - Viga bajo la losa / viga chata VCH (línea oculta)
  - Vigueta 0.10 (nervio) - casetones entre viguetas
  - Dirección de viguetas, aligerado h = 0.20
  - Acero de refuerzo (rep.): trazo corto = gancho 90°
  - Borde de losa

PROYECTO:  
CASA SAN JERÓNIMO - REDISEÑO ESTRUCTURAL 4 x 3  
5 niveles (Cimentación -2.00, N1 ±0.00 ... N5 +11.00)

ESPECIALIDAD: ESTRUCTURAS  
LOSA ALIGERADA - NIVEL 4 (NPT +8.40)  
PLANTA, CORTES, DETALLE VCH Y CUADRO DE ACERO

ESCALA: INDICADA  
FECHA: SET. 2026

FUENTE: modelo IFC 'Project s.j.fc' (Revit 2022, IFC4, 26-09-2026)

PROFESIONAL RESPONSABLE:  
CIP

REVISÓ: